


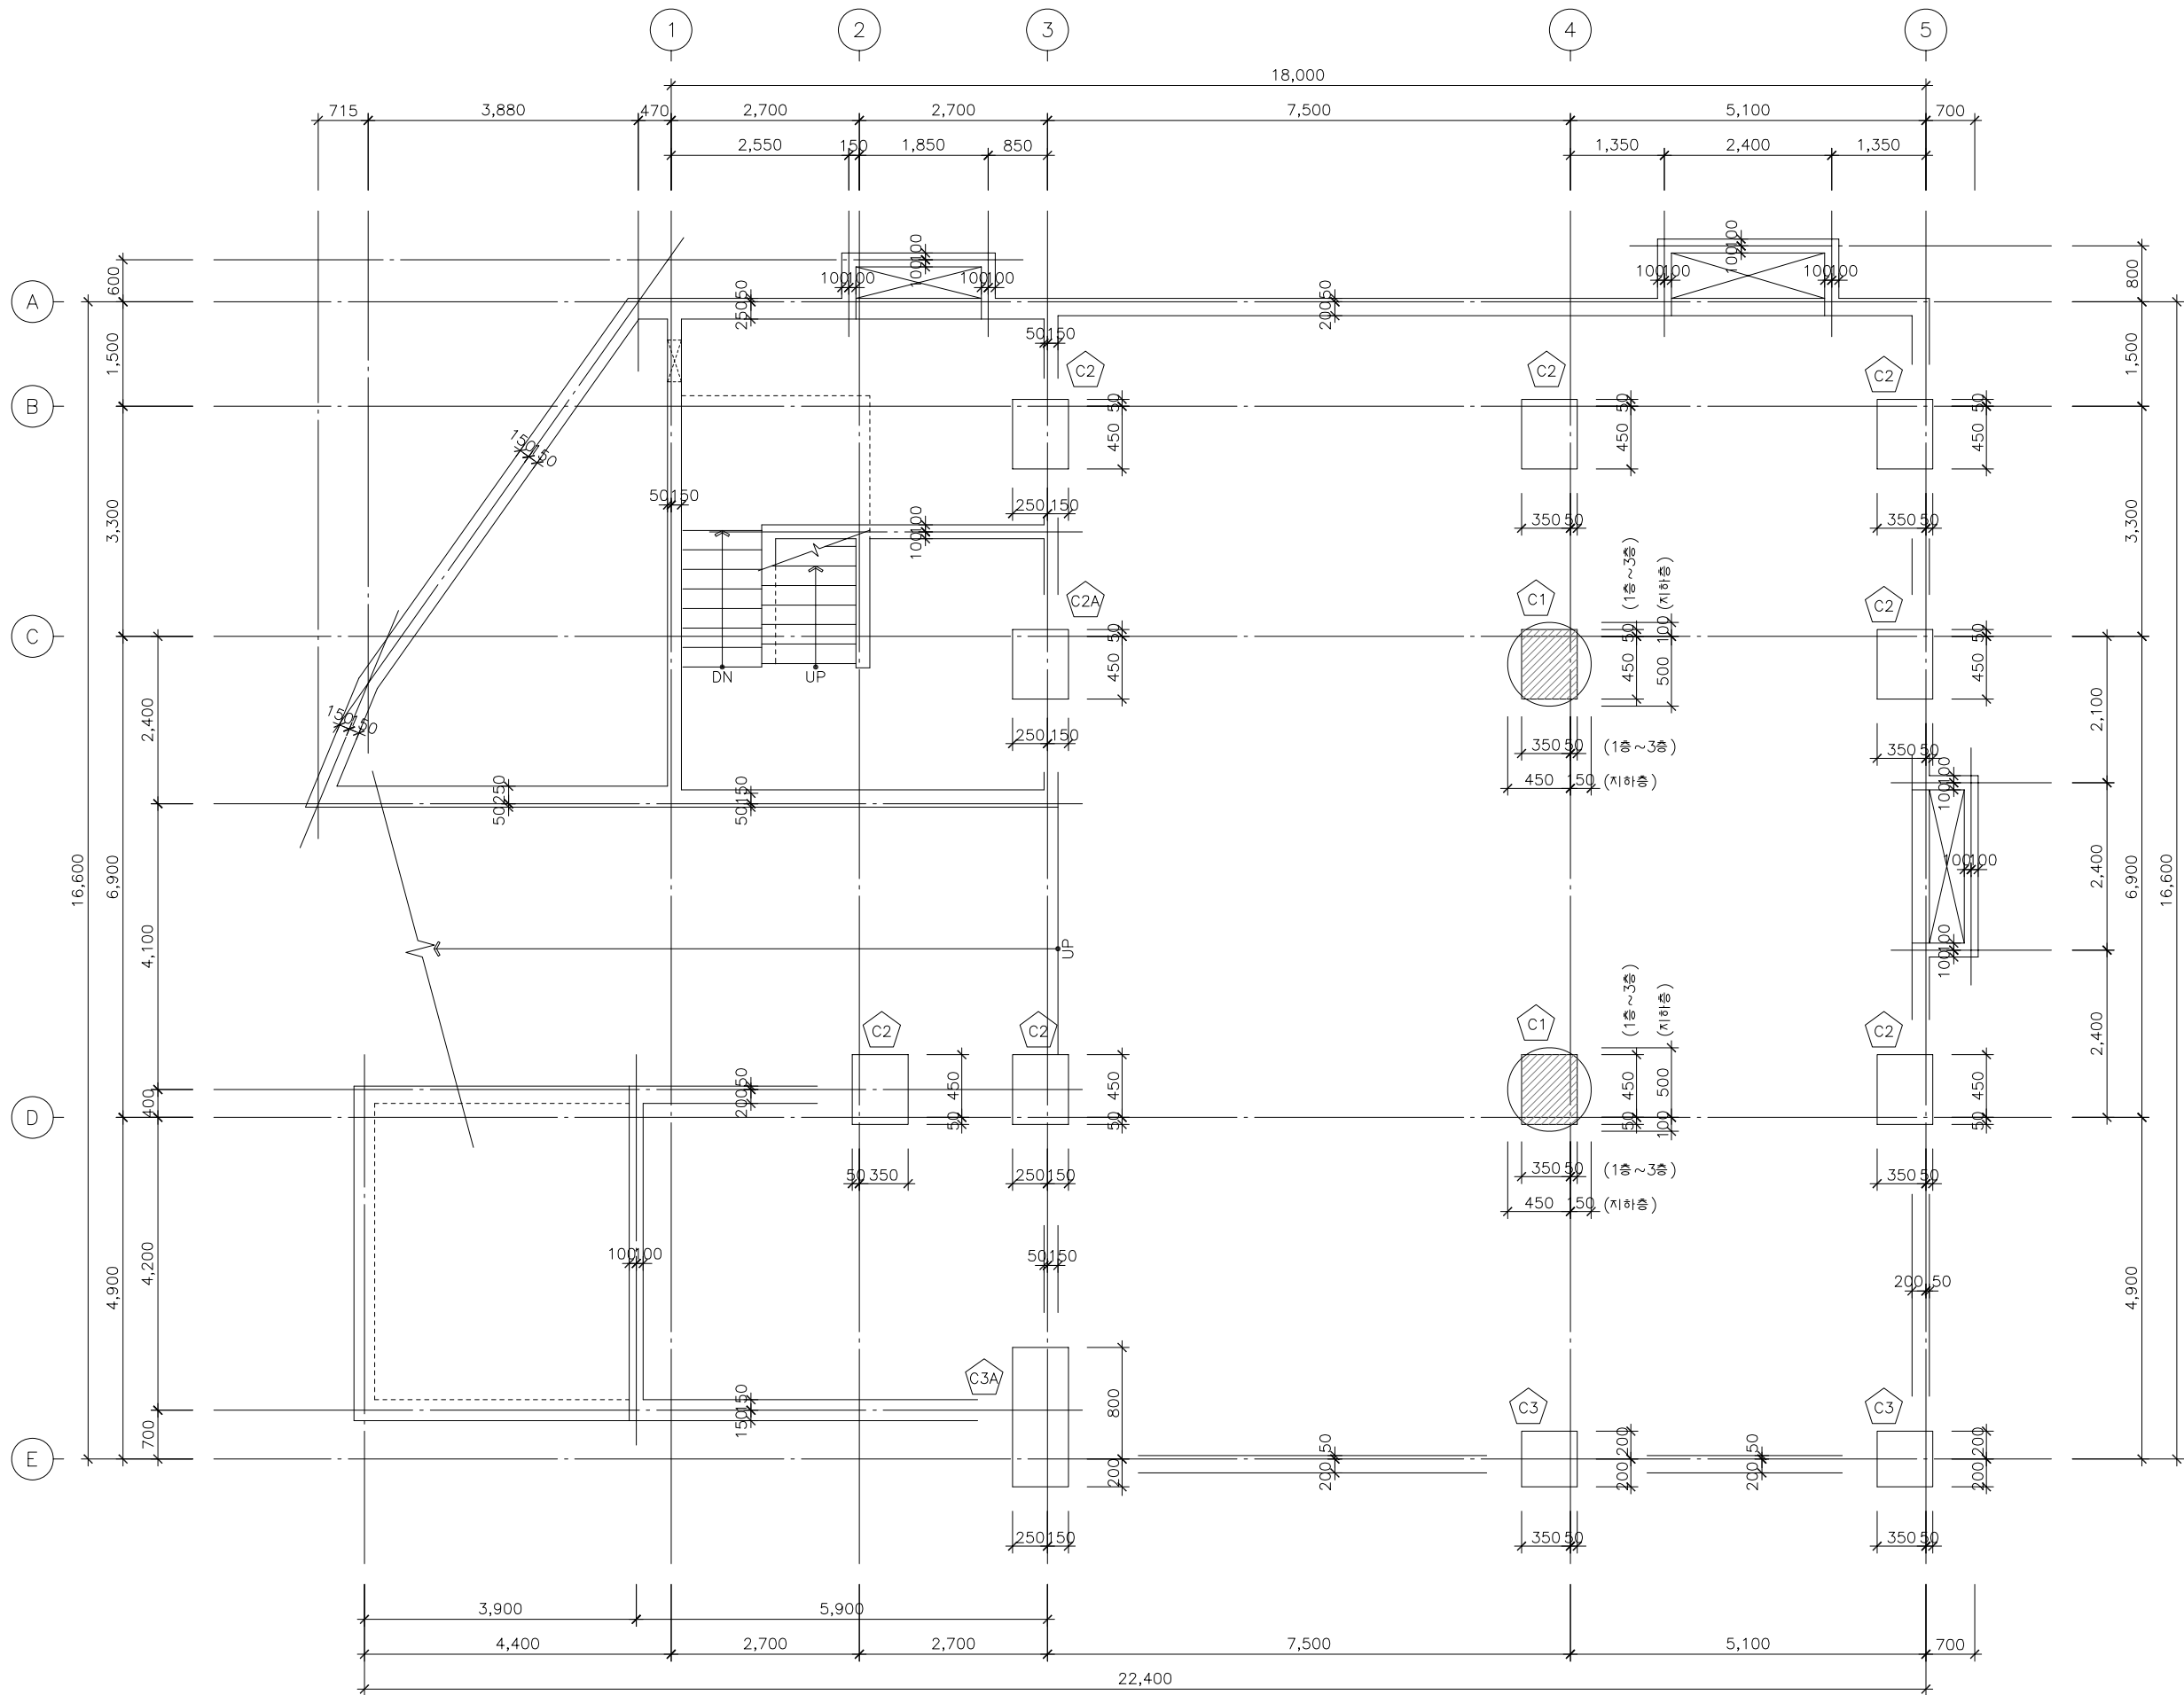

1 주심도
축척 : 1/50, 100

NOTES

이 도면은 고려전산(주)의
프로그램 교육용으로 작성
된 도면입니다.

이 도면의 저작권은 고려전
산(주)에 있으며 사전 승인
없이 무단전재 및 재배포할
경우, 관련 법령에 의거 제
재를 받을 수 있습니다.
또한, 본사의 교육 이외 용
도로의 사용을 금합니다.

REV. NO.	DATE	REVISION DESCRIPTION
-------------	------	-------------------------

DRAWN BY

DESIGNED BY

CHECKED BY

CIVIL ENGINEERING

ARCHITECTURAL

STRUCTURAL

MERCHANICAL

ELECTRICAL

APPROVED BY

PROJECT NO.

SCALE
A3:1/100

DATE

DRAWING NO.
S-01


SHEET NO.

BUILDING NAME



PROJECT

DRAWING TITLE


주심도

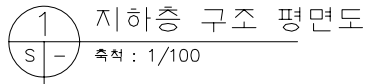

8. 웅벽 / 바닥 JOINT KEY

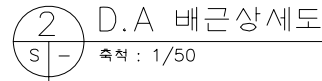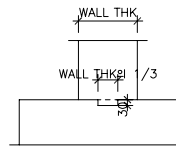

NOTES		
이 도면은 고려전산(주)의 프로그램 교육용으로 작성된 도면입니다. 이 도면의 저작권은 고려전산(주)에 있으며 사전 승인 없이 무단전재 및 재배포할 경우, 관련 법령에 의거 제재를 받을 수 있습니다. 또한, 본사의 교육 이외 용도로의 사용을 금합니다.		
REV. NO.	DATE	REVISION DESCRIPTION
DRAWN BY		
DESIGNED BY		
CHECKED BY		
CIVIL ENGINEERING		
ARCHITECTURAL		
STRUCTURAL		
MECHANICAL		
ELECTRICAL		
APPROVED BY		
PROJECT NO.		
SCALE	A3:1/100	
DATE		
DRAWING NO.	S-02	
SHEET NO.		
BUILDING NAME		
PROJECT		
DRAWING TITLE		
지하층 구조 평면도		

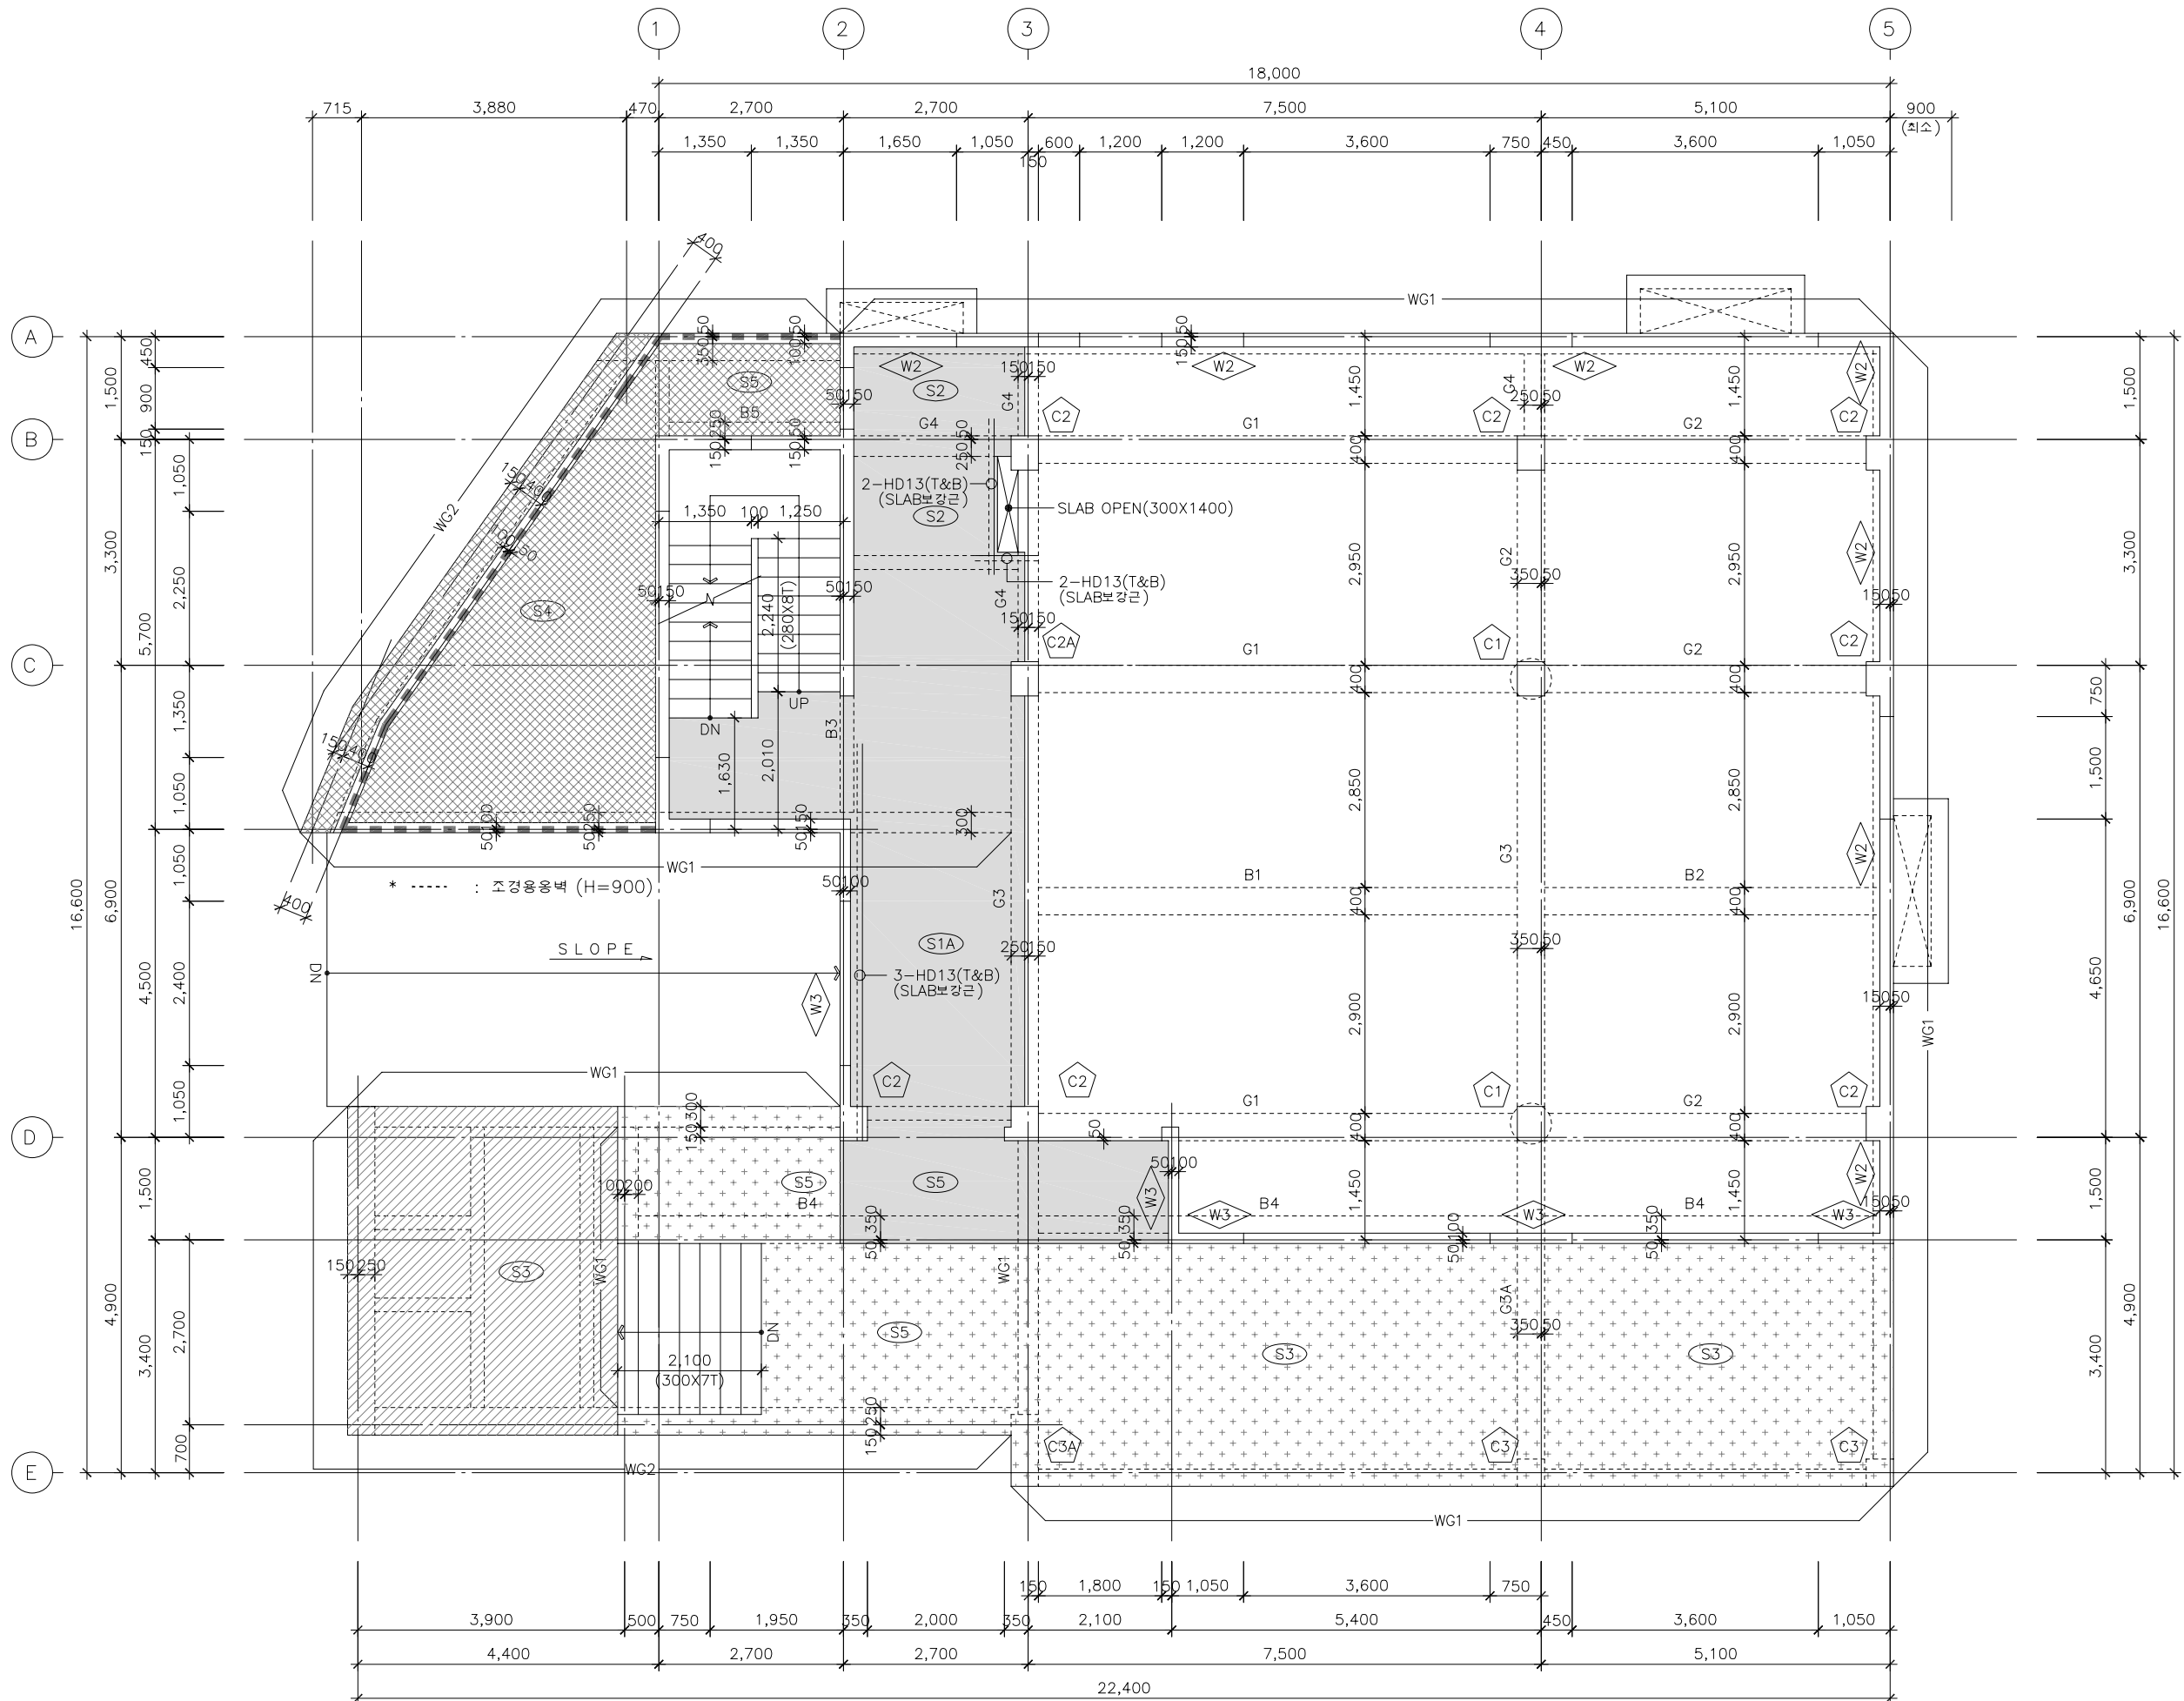

1층 구조 평면도
축척 : 1/100

* NOTE : 1. 표기 없는 모든 WALL : W1
2. 표기 없는 모든 SLAB : 1S1
3. 표기 없는 모든 계단 SLAB : SS1


- 4. : 1층 S.L - 50
- 5. : 1층 S.L - 400
- 6. : 1층 S.L - 1000
- 7. : 1층 S.L - 1600

NOTES

이 도면은 고려전산(주)의 프로그램 교육용으로 작성된 도면입니다.

이 도면의 저작권은 고려전산(주)에 있으며 사전 승인 없이 무단전재 및 재배포할 경우, 관련 법령에 의거 제재를 받을 수 있습니다. 또한, 본사의 교육 이외 용도로의 사용을 금합니다.

REV. NO.	DATE	REVISION DESCRIPTION
DRAWN BY		
DESIGNED BY		
CHECKED BY		
CIVIL ENGINEERING		
ARCHITECTURAL		
STRUCTURAL		
MECHANICAL		
ELECTRICAL		
APPROVED BY		
PROJECT NO.		
SCALE A3:1/100		
DATE		
DRAWING NO. S-03		
SHEET NO.		
BUILDING NAME		
PROJECT		
DRAWING TITLE 1층 구조 평면도		

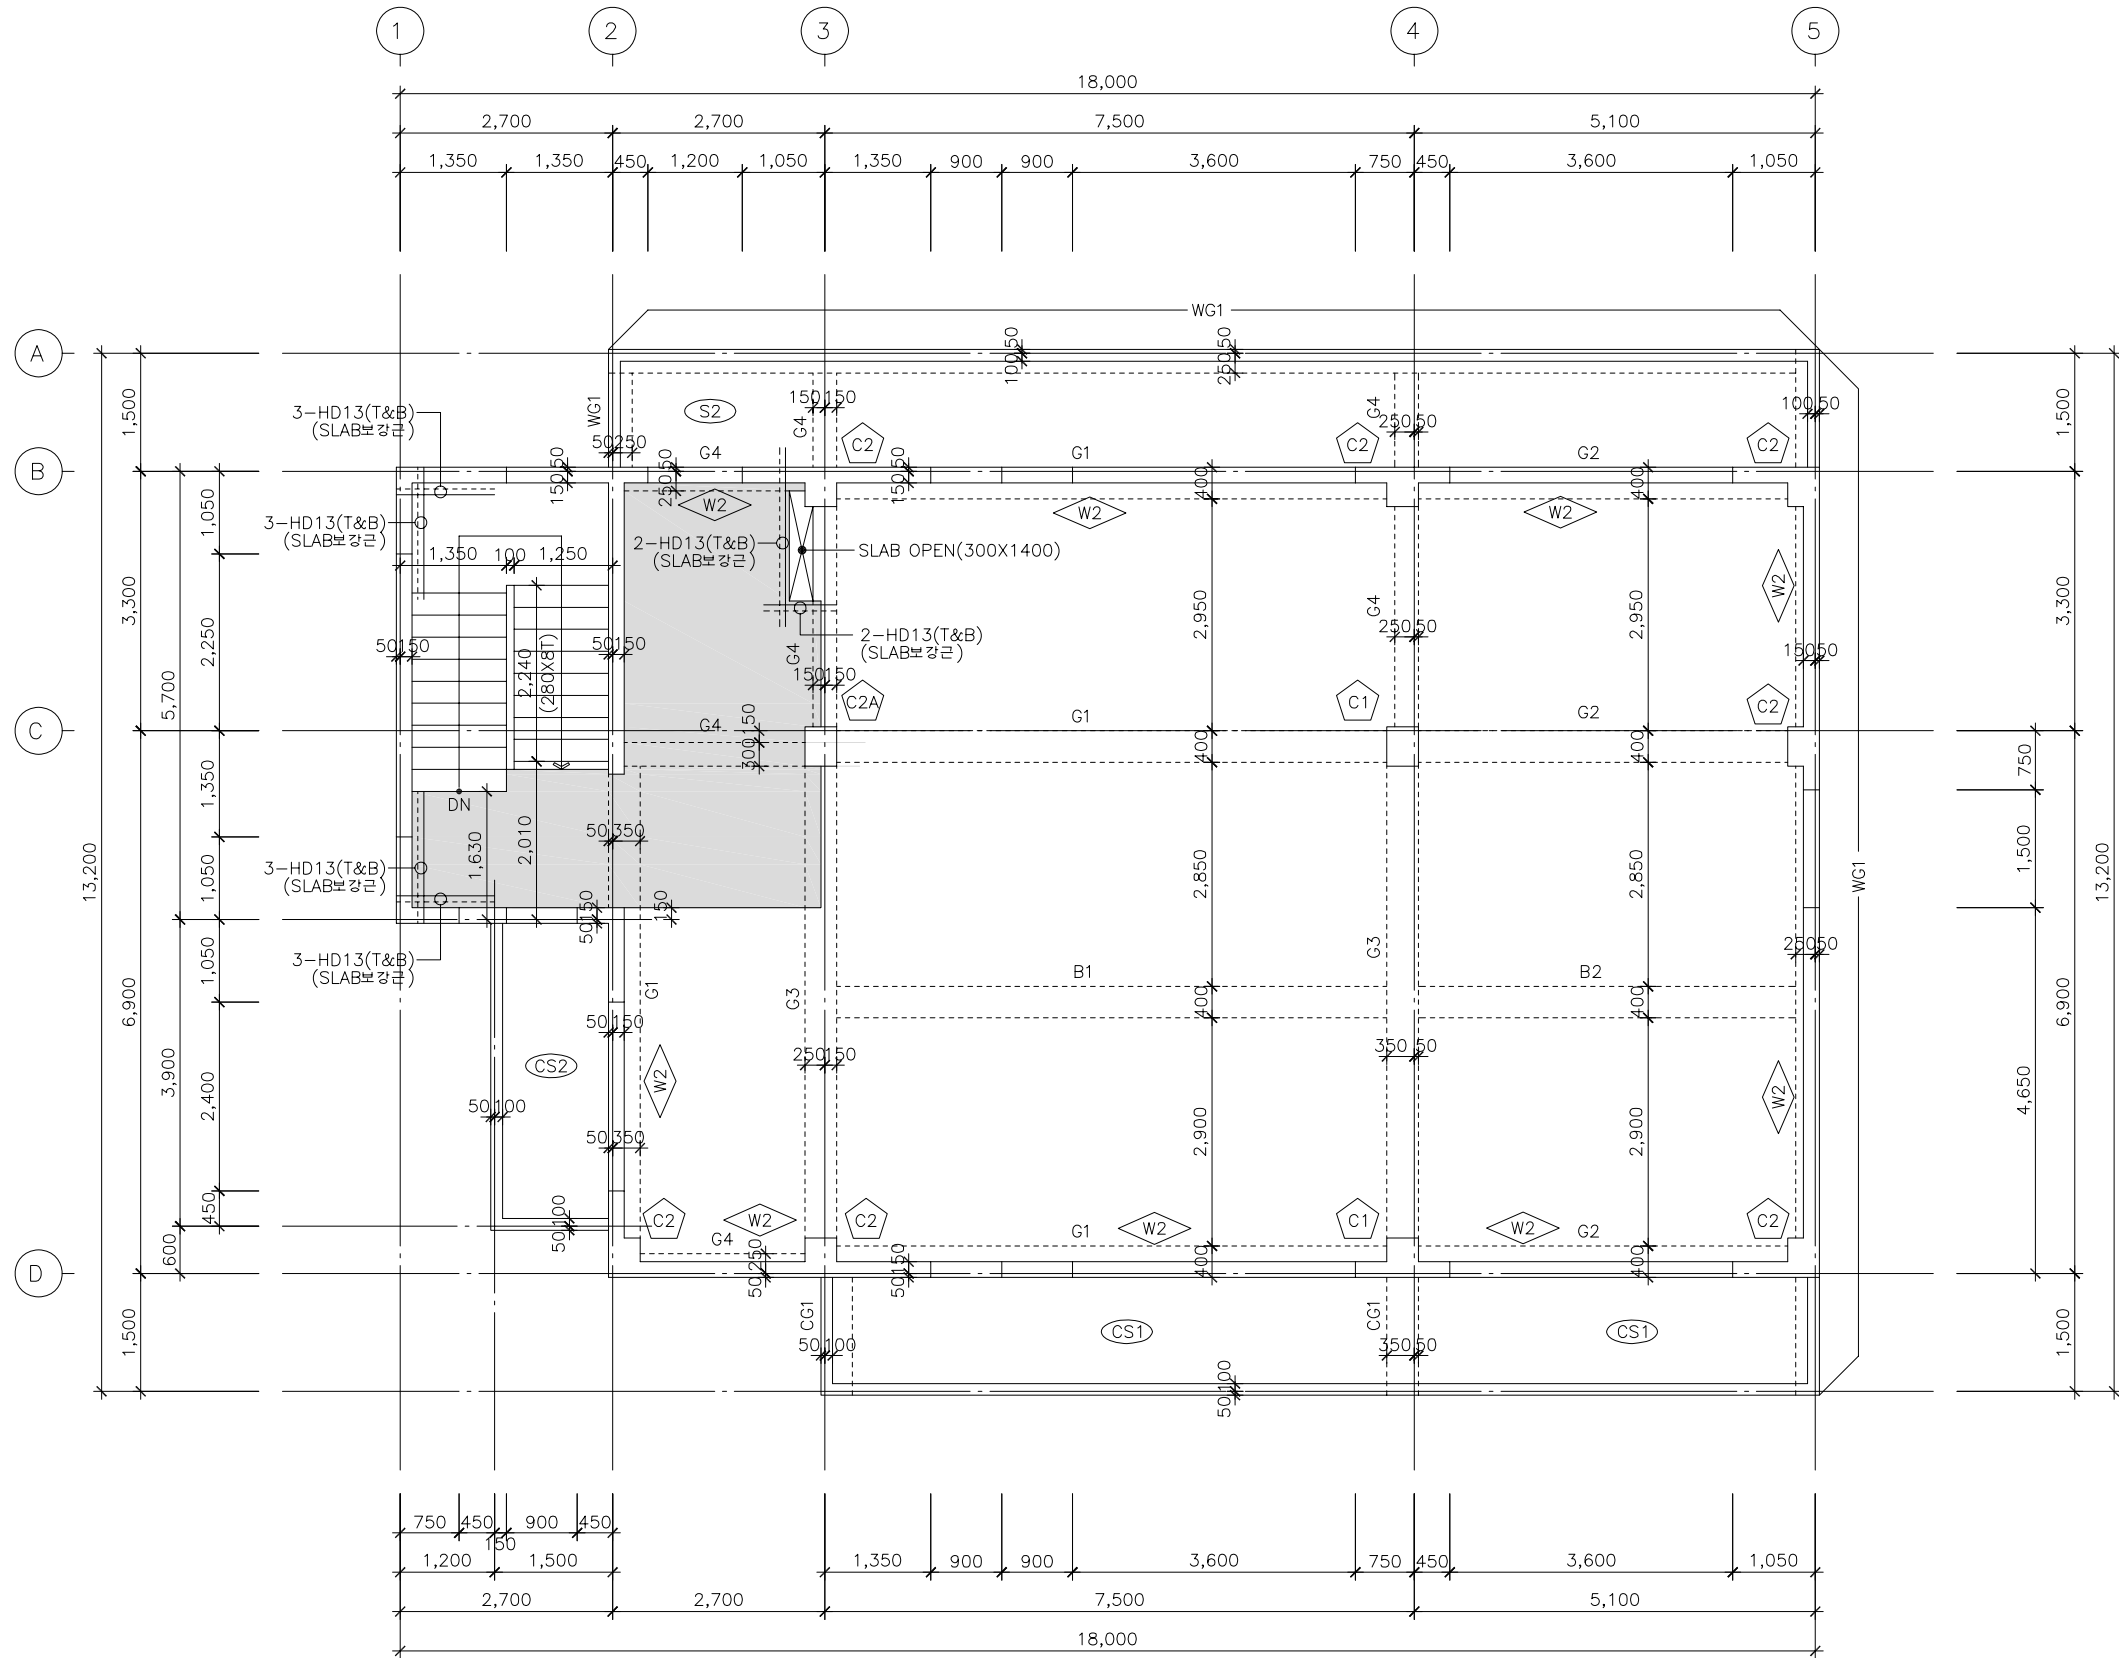

1 3층 구조 평면도
축척 : 1/100

- * NOTE : 1. 표기 없는 모든 WALL : W1
2. 표기 없는 모든 SLAB : S1
3. 표기 없는 모든 계단 SLAB : SS1
4. : 3층 S.L - 50

NOTES

이 도면은 고려전산(주)의
프로그램 교육용으로 작성
된 도면입니다.

이 도면의 저작권은 고려전
산(주)에 있으며 사전 승인
없이 무단전재 및 재배포할
경우, 관련 법령에 의거 제
재를 받을 수 있습니다.
또한, 본사의 교육 이외 용
도로의 사용을 금합니다.

REV. NO.	DATE	REVISION DESCRIPTION
----------	------	----------------------

DRAWN BY

DESIGNED BY

CHECKED BY

CIVIL ENGINEERING

ARCHITECTURAL

STRUCTURAL

MERCHANICAL

ELECTRICAL

APPROVED BY

PROJECT NO.

SCALE
A3:1/100

DATE

DRAWING NO.
S-05


SHEET NO.

BUILDING NAME

PROJECT

DRAWING TITLE







3층 구조 평면도

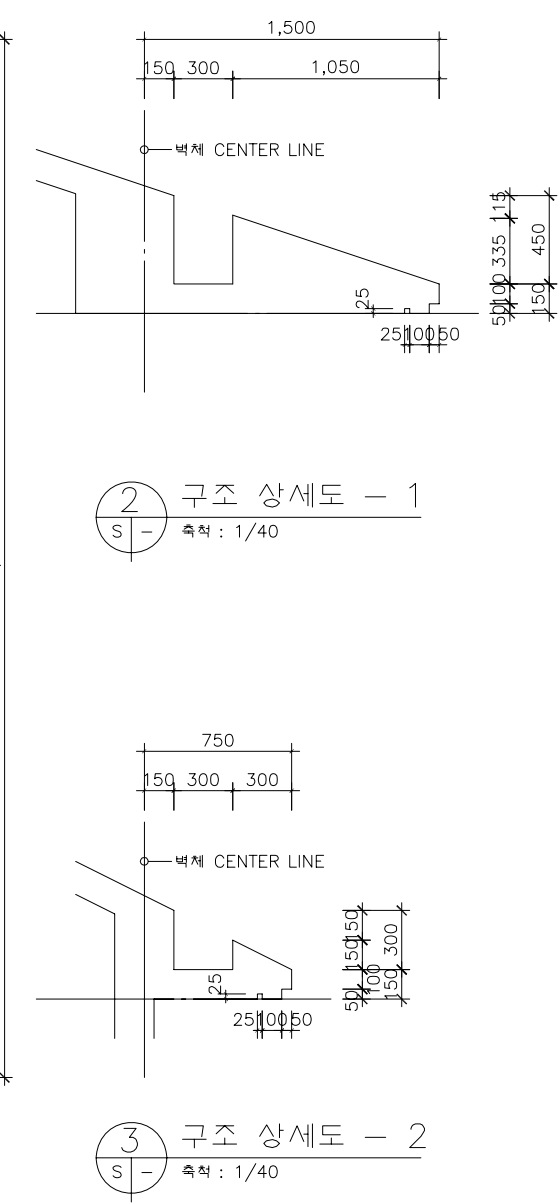

* NOTE : 1. 표기 없는 모든 WALL : W1
2. 표기 없는 모든 SLAB : RS1

NOTES		
이 도면은 고려전산(주)의 프로그램 교육용으로 작성된 도면입니다. 이 도면의 저작권은 고려전산(주)에 있으며 사전 승인 없이 무단전재 및 재배포할 경우, 관련 법령에 의거 제재를 받을 수 있습니다. 또한, 본사의 교육 이외 용도로의 사용을 금합니다.		
REV. NO.	DATE	REVISION DESCRIPTION
DRAWN BY		
DESIGNED BY		
CHECKED BY		
CIVIL ENGINEERING		
ARCHITECTURAL		
STRUCTURAL		
MERCHANCIAL		
ELECTRICAL		
APPROVED BY		
PROJECT NO.		
SCALE		
A3:1/100		
DATE		
DRAWING NO.		
S-06		
SHEET NO.		
BUILDING NAME		
PROJECT		
DRAWING TITLE		
지붕 구조 평면도		

보 일람표	명칭	1G1, 2G1, 3G1, RG1		1G2, 2G2, 3G2, RG2		철근배근 1. CUT TYPE STIRRUP 1. SINGLE 형태 2. DOUBLE 형태
	형식					
구분	내 / 외단부	중 앙 부	A L L			
상부근	5 - HD19	3 - HD19	3 - HD19			
하부근	3 - HD19	5 - HD19	2 - HD19			
스피	HD10 @200	HD10 @300	HD10 @200			
명칭	1G3, 2G3, 3G3		1G4, 2G4, 3G4, RG4			
형식						
구분	내 / 외단부	중 앙 부	A L L			
상부근	9 - HD19	3 - HD19	3 - HD19			
하부근	3 - HD19	9 - HD19	3 - HD19			
스피	HD10 @150	HD10 @200	HD10 @250			
명칭	RG3		1G3A		1WG1, 2WG1, 3WG1, RWG1	
형식						
구분	내 / 외단부	중 앙 부	내 / 외단부	중 앙 부	A L L	
상부근	6 - HD19	4 - HD19	9 - HD19	3 - HD19	3 - HD19	
하부근	4 - HD19	6 - HD19	3 - HD19	9 - HD19	3 - HD19	
스피	HD10 @200	HD10 @250	HD13 @150	HD13 @200	HD10 @250	
명칭	1WG2, 2WG2, 3WG2, RWG2		2CG1, 3CG1			
형식						
구분	A L L		내 단 부	중 앙 부	외 단 부	
상부근	3 - HD19		6 - HD19	4 - HD19	3 - HD19	
하부근	3 - HD19		3 - HD19	3 - HD19	3 - HD19	
스피	HD10 @250		HD10 @250	HD10 @250	HD10 @250	
명칭	1B1, 2B1, 3B1, RB1		1B2, 2B2, 3B2, RB2		1B3, 2B3, 3B3, RB3	
형식						
구분	내 단 부	중 앙 부	외 단 부	A L L	A L L	
상부근	5 - HD19	3 - HD19	3 - HD19	3 - HD19	2 - HD16	
하부근	3 - HD19	5 - HD19	3 - HD19	2 - HD19	2 - HD16	
스피	HD10 @200	HD10 @300	HD10 @200	HD10 @200	HD10 @150	
명칭	1B4		1B5			
형식						
구분	내 단 부	중 앙 부	A L L			
상부근	7 - HD19	4 - HD19	5 - HD19			
하부근	4 - HD19	7 - HD19	5 - HD19			
스피	HD10 @200	HD10 @250	HD13 @250			

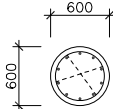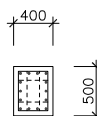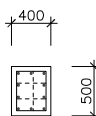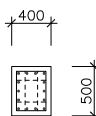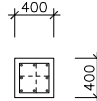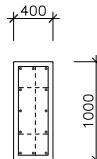부 호	상 면	지 하 상	부 호	상 면	1 층 ~ 3 층	부 호	상 면	지 하 상 ~ 3 층	부 호	상 면	지 하 상 ~ 3 층
											
주 근	10 - HD19	주 근	14 - HD19	주 근	10 - HD19	주 근	14 - HD19				
대 근	HD10 @250	대 근	HD10 @250	대 근	HD10 @250	대 근	HD10 @250				
보조대근	HD10 @500	보조대근	HD10 @500	보조대근	HD10 @500	보조대근	HD10 @500				
부 호	상 면	지 하 상	부 호	상 면	지 하 상	부 호	상 면	지 하 상	부 호	상 면	지 하 상
											
주 근	8 - HD19	주 근	12 - HD19	주 근		주 근					
대 근	HD10 @250	대 근	HD10 @250	대 근		대 근					
보조대근	HD10 @500	보조대근	HD10 @500	보조대근		보조대근					

벽 체 OPENING 보강

600 OPEN 600

600

OPEN

1-HD13

1-HD13

1-HD13

1-HD13

1-HD13(L=800)

1-HD13

1-HD13

1-HD13(L=800)

상부근

하부근

NOTES

1. $F_c = 210\text{kgf/cm}^2$
2. $f_y = 4000\text{kgf/cm}^2$
3. 지내력은 20TON/m^2 로 가정.

이 도면은 고려전산(주)의
프로그램 교육용으로 작성
된 도면입니다.

이 도면의 저작권은 고려전산(주)에 있으며 사전 승인 없이 무단전재 및 재배포할 경우, 관련 법령에 의거 제재를 받을 수 있습니다.
또한, 본사의 교육 이외 용도로의 사용을 금합니다.

REV. NO.	DATE	REVISION DESCRIPTION
-------------	------	-------------------------

DRAWN BY

DESIGNED BY

CHECKED BY

CIVIL ENGINEERING

ARCHITECTURAL

STRUCTURAL

MERCHANICAL

ELECTRICAL

APPROVED BY

PROJECT NO.

SCALE

NONE

DRAWING NO.

S-07

SHEET NO.

BUILDING NAME

PROJECT

DRAWING TITLE

구조 일람표 - 1

승강기 일람표

옹벽 TYPE

부 호	TYPE	두 개 (THK)	수 직 철 근			수 평 철 근		H	비 고
			A	B	C	D	E		
W1	A	200	HD13 @300	HD13 @300		HD13 @300	HD13 @300		
W2	A	200	HD10 @300	HD10 @300		HD10 @300	HD10 @300		
W3	A	150	HD10 @300	HD10 @300		HD10 @300	HD10 @300		
RW1	B	250	HD13 @300	HD13 @300	HD13 @300	HD13 @300	HD13 @300	3350	
RW2	B	300	HD13 @200	HD13 @150	HD13 @200	HD13 @300	HD13 @300	4850	
DW1	C	200	HD13 @200	HD13 @200		HD13 @250	HD13 @250	2000	
조경용벽(지상)	D	150	HD10 @300	HD10 @300		HD10 @300	HD10 @300		

계단 배근도

계 단 TYPE E

The diagram illustrates the reinforcement layout for a staircase, labeled 'TYPE - A'. It shows a side view of the stairs with reinforcement bars (A, B, C, D, E, F) and dimensions. The total length of the stairs is denoted as L . The thickness of the slab is denoted as THK . The distance from the top of the stairs to the first reinforcement bar is $0.3L$. The distance between the first and second reinforcement bars is $0.25L$. The distance between the last two reinforcement bars is $0.3L$. The distance from the last reinforcement bar to the bottom of the stairs is $0.25L$. The reinforcement bars are labeled A, B, C, D, E, and F. The diagram is labeled 'TYPE - A'.

부 호	TYPE	두 개	A	B	C	D	E	F	비 고
SS1	A	150	HD13 @200	HD13 @200	HD13 @200	HD13 @200	HD13 @250	4 - HD13	

SLAB TYPE

TYPE - A

TYPE - B

TYPE - C

TYPE - D

————— : 상 부筋
- - - - - : 하 부筋

SLAB 일람표	부 호	TYPE	두 개	단 변 방 향 철 근					비 고	
				X1	X2	X3	X4	X5		
				장 변 방 향 철 근						
				Y1	Y2	Y3	Y4	Y5		
1S1, 2S1, 3S1	A	150		HD10 @400	HD10 @400	HD10 @400	HD10 @200	HD10 @200		
				HD10 @500	HD10 @500	HD10 @500	HD10 @300	HD10 @300		
RS1	C	150		HD10 @200	—	HD10 @200	—	—		
				HD10 @300	—	HD10 @300	—	—		
1S2, 2S2, 3S2	C	150		HD10 @200	—	HD10 @200	—	—		
				HD10 @300	—	HD10 @300	—	—		
1S3	B	150		HD13 @400	HD10 @400	HD10 @400	HD10+13 @200	HD10+13 @200		
				HD13 @600	HD10 @600	HD10 @600	HD10 @300	HD10 @300		
1S4	B	200		HD13 @300	HD13 @300	HD13 @300	HD13 @200	HD13 @200		
				HD13 @500	HD13 @500	HD13 @500	HD13 @300	HD13 @300		
1S5	B	150		HD13 @400	HD10 @400	HD10 @400	HD10 @200	HD10 @200		
				HD10 @500	HD10 @500	HD10 @500	HD10 @300	HD10 @300		
2CS1, 3CS1	D	150		HD10+13 @200	—	HD10 @200	—	—		
				HD10 @300	—	HD10 @300	—	—		
2CS2, 3CS2	D	150		HD10+13 @100	—	HD10 @100	—	—		
				HD10 @200	—	HD10 @200	—	—		
1S1A	C	150		HD13 @200	—	HD13 @200	—	—		
				HD13 @200	—	HD13 @200	—	—		
RPS1 (RAMP 부분)	C	150		HD13 @150	—	HD13 @150	—	—		
				HD10 @300	—	HD10 @300	—	—		
BS1 (오수처리시설 상부)	C	150		HD10 @200	—	HD10 @200	—	—		
				HD10 @300	—	HD10 @300	—	—		

- NOTES
1. $F_c = 210\text{kgf/cm}^2$

2. $f_y = 4000\text{kgf/cm}^2$

3. 지내력은 20TON/m^2 로 가정.

이 도면은 고려전산(주)의 프로그램 교육용으로 작성된 도면입니다.

이 도면의 저작권은 고려전산(주)에 있으며 사전 승인 없이 무단전제 및 재배포할 경우, 관련 법령에 의거 제재를 받을 수 있습니다. 또한, 본사의 교육 이외 용도로의 사용을 금합니다.

REV. NO.	DATE	REVISION DESCRIPTION
DRAWN BY		
DESIGNED BY		
CHECKED BY		
CIVIL ENGINEERING		
ARCHITECTURAL		
STRUCTURAL		
MECHANICAL		
ELECTRICAL		
APPROVED BY		
PROJECT NO.		
SCALE	NONE	
DATE		
DRAWING NO.	S-08	
SHEET NO.		
BUILDING NAME		
PROJECT		
DRAWING TITLE		
구조 일람표 - 2		