


■ 건축 개요

건 축 주		
대 지 위 치		
대 지 면 적	465.00 M2	
지 역 . 지 구	제 1 종 일 반 주 거 지 역, 지 구 단 위 계 획 구 역	
도 로 현 황	동측면 4 M 보차혼용도로에 접함	
건 축 면 적	219.15 M2	
건 폐 율	47.13 % (219.15 / 465.00 x 100) < 60 % (법 정)	
연 면 적	897.42 M2	
용적율산정용 연면적	600.75 M2	
용 적 률	129.19%(600.75/465.00X100)<120%(법정 기준용적율)+20%(완화용적율)=140% * 완화 용적율 20 % : 대지교환 이행, 경사지붕 - 각 10 %	
용 도	제1종 / 제2종 근린생활시설	
규 모	지 하 1 층 / 지 상 3 층	
주차산정 면적	1. 제1종 / 제2종 근린생활시설 : 600.75 M2	
주 차 대 수	법 정	제1종 / 제2종 근린생활시설 : 시설면적 60 M2 당 1대 = 600.75 / 60(M2) = 10.01, * 10 대
	계 획	10 대 (자주식 주차)
조 경 면 적	법 정	연면적 1000 M2 미만 : 대지 면적의 10 % (46.50 M2) 이상
	계 획	48.30 M2 (대지 면적의 10.39 %)
정 화 조	오 수 처 리 시 설 (200 인 용, 40 M3 / 일)	
구 조	철 근 콘 크 리 트 조	

■ 층 별 / 용 도 별 면 적 표

층 별	면 적	용 도	비 고
지 하 층	88.77 M2	펌프실, 오수처리시설	용적율 산정시 제외
지 하 층	207.90 M2	주 차 장	용적율 산정시 제외
지 상 1 층	210.15 M2	제1종 근린생활시설 (근린생활시설)	
지 상 2 층	219.15 M2	제2종 근린생활시설 (사 무 소)	
지 상 3 층	171.45 M2	제2종 근린생활시설 (사 무 소)	
연 면 적	897.42 M2	용적율산정용 연면적	600.75 M2

■ 안 내 도

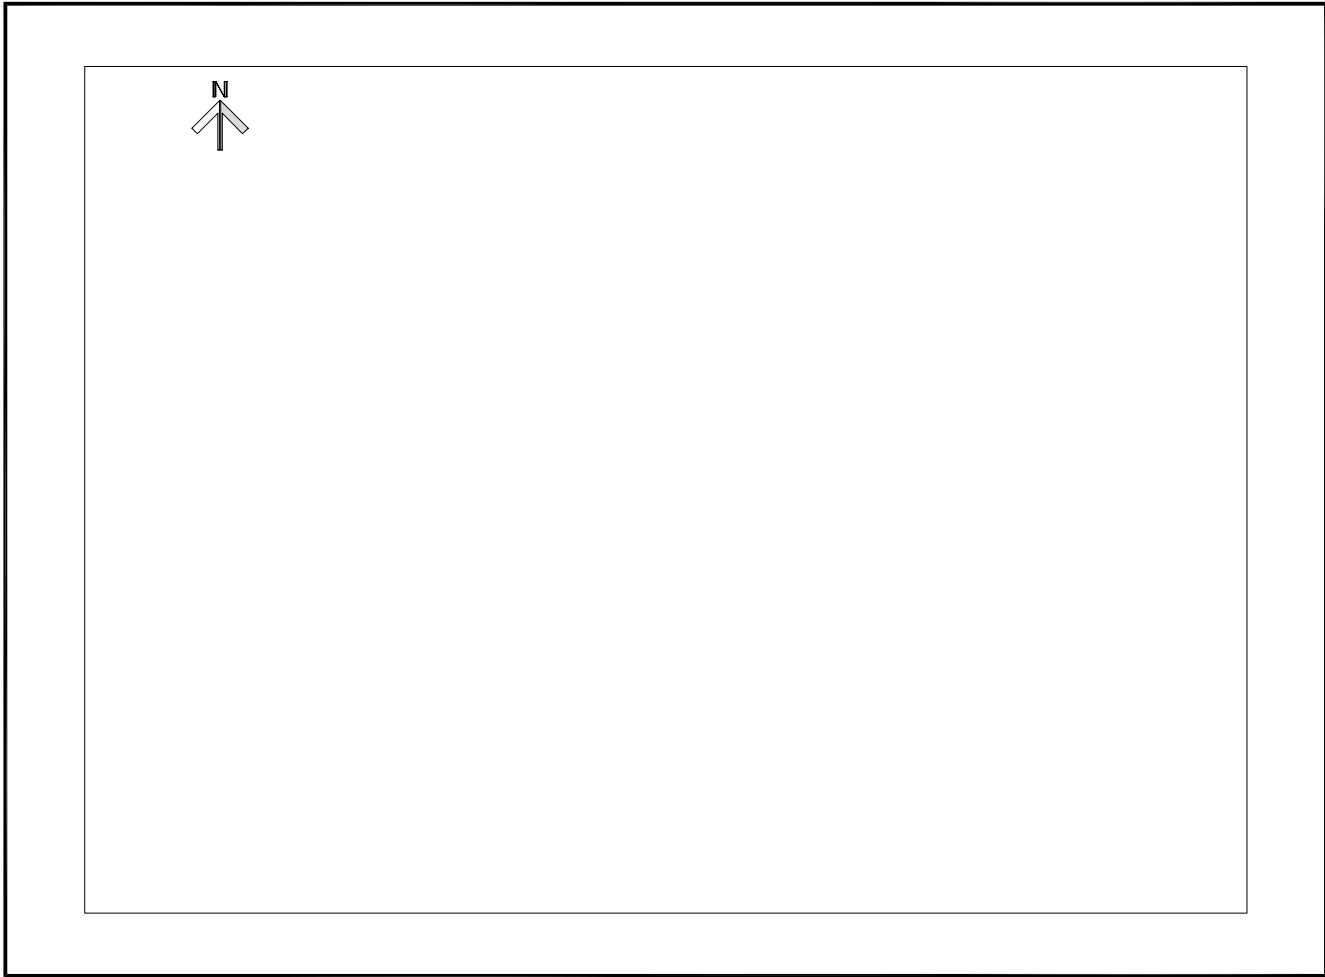

■ 지 구 단 위 계 획 의 이 행

구 분	지구단위계획 내용	비 고
용 도 지 역	제 1 종 일 반 주 거 지 역	
건축물의 용도 (허용용도)	- 제1종 근린생활시설 - 제2종 근린생활시설 중 사무소	신청 건축물의 용도 : 제1종 근린생활시설, 제2종 근린생활시설(사무소)
건 폐 율	60 % 이하	이행함(47.13 %)
용 적 률	120 % 이하 (허용용적율 140% 이하)	이행함(129.19 %)
층수(높이) 제한	3 층, 10 M 이하 (경사지붕 : 높이 기준을 처마 끝선으로 함)	이 행 함 (지붕: 경사지붕, 높이: 9.64M)
지 하 층	지하 주차장 허용	이행함(지하 주차장)
부설주차장 기준	제1종 / 제2종 근린생활시설 : 시설면적 60 M2 당 1대 = 600.75 / 60(M2) = 10.01, * 10 대	이행함(10 대)
행위완화 적용항목	대지교환 이행시, 경사지붕 - 각 10 %	이 행 함
완화 용적율	제1종 일반주거지역 : 기준용적율 120% + 완화용적율 (단, 중복적용한 경우 최대 150%를 초과할 수 없음)	이 행 함 (용적율 140%를 기준으로 적용)
건축 한계선	도로경계선에서 1M 후퇴	이 행 함

NOTES

이 도면은 고려전산(주)의 프로그램 교육용으로 작성된 도면입니다.

이 도면의 저작권은 고려전산(주)에 있으며 사전 승인 없이 무단전재 및 재배포할 경우, 관련 법령에 의거 제재를 받을 수 있습니다. 또한, 본사의 교육 이외 용도로의 사용을 금합니다.

REV. NO.	DATE	REVISION DESCRIPTION
----------	------	----------------------

DRAWN BY

DESIGNED BY

CHECKED BY

CIVIL ENGINEERING

ARCHITECTURAL

STRUCTURAL

MERCHANICAL

ELECTRICAL

APPROVED BY

PROJECT NO.

SCALE
NONE

DATE

DRAWING NO.
A-01

SHEET NO.

BUILDING NAME

PROJECT

DRAWING TITLE

건축개요, 안내도,
층별/용도별 면적표

재 료 마 감 표

층 별	실 명	마감번호	바 닥		걸 레 받 이		상세번호	벽		상세번호	천 정 틀			상세번호	비 고
			바 탕	마 감	바 탕	마 감		바 탕	마 감		바 탕	마 감	천 정 틀		
지 하 층	복 도	-	시멘트 몰탈	THK30 화강석울갈기	시멘트 몰탈	세라민페인트	-	시멘트 몰탈	조합페인트	-	경량철골 천정을 + THK9.5 석고보드	THK9.5 MDF위 조합페인트	M-BAR	-	C.H = 2500
	계 단 실	-	시멘트 몰탈	THK30 화강석울갈기	시멘트 몰탈	세라민페인트	-	시멘트 몰탈	조합페인트	-	시멘트 몰탈	조합페인트	-	-	
	FAN ROOM	-	THK150 보호콘크리트	THK3 에폭시라이닝	시멘트 몰탈	세라민페인트	-	시멘트 몰탈	수성 페인트	-	경량철골 천정을 + THK9.5 석고보드	THK6 아스텍스	M-BAR	-	C.H = 2500
	펌 프 실	-	THK150 보호콘크리트	THK3 에폭시라이닝	시멘트 몰탈	세라민페인트	-	시멘트 몰탈	수성 페인트	-	시멘트 몰탈	수성 페인트	-	-	
	주 차 장	-	THK150 보호콘크리트	후로아하드너	시멘트 몰탈	세라민페인트	-	시멘트 몰탈	수성 페인트	-	THK85 드라이비트	FINAL COAT	-	-	
	소화용수탱크	-	콘크리트 구체	에폭시 코팅	시멘트 몰탈	에폭시 코팅	-	시멘트 몰탈	에폭시 코팅	-	시멘트 몰탈	에폭시 코팅	-	-	
	정화조관리실	-	콘크리트 구체	제물치장 마감	-	-	-	액체방수 1종	수성 페인트	-	액체방수 1종	수성 페인트	-	-	
	오수처리시설	-	콘크리트 구체	액체방수 1종+에폭시 코팅	-	-	-	콘크리트 구체	액체방수 1종+에폭시 코팅	-	콘크리트 구체	액체방수 1종+에폭시 코팅	-	-	
1 층	방 품 실	-	시멘트 몰탈	THK30 화강석울갈기	시멘트 몰탈	THK12 화강석울갈기	-	콘크리트 OR 조적	THK30 화강석울갈기	-	경량철골 천정을 + THK9.5 석고보드	THK9.5 MDF위 조합페인트	M-BAR	-	C.H = 2500
	복 도	-	시멘트 몰탈	THK30 화강석울갈기	시멘트 몰탈	세라민페인트	-	시멘트 몰탈	조합페인트	-	경량철골 천정을 + THK9.5 석고보드	THK9.5 MDF위 조합페인트	M-BAR	-	C.H = 2500
	계 단 실	-	시멘트 몰탈	THK30 화강석울갈기	시멘트 몰탈	세라민페인트	-	시멘트 몰탈	조합페인트	-	시멘트 몰탈	조합페인트	-	-	
	근린생활시설	-	제물치장 마감	* 입주자 공사	시멘트 몰탈	세라민페인트	-	시멘트 몰탈	수성 페인트	-	제물치장 콘크리트	* 입주자 공사	-	-	
	화 장 실	-	액체방수 1종	바닥타일(300X300)	-	-	-	액체방수 1종(H=1500)	벽타일(300X300)	-	경량철골 천정을 + THK12.5 내수석고보드	아크릴 페인트	M-BAR	-	C.H = 2300
2 층	복 도	-	시멘트 몰탈	THK30 화강석울갈기	시멘트 몰탈	세라민페인트	-	시멘트 몰탈	조합페인트	-	경량철골 천정을 + THK9.5 석고보드	THK9.5 MDF위 조합페인트	M-BAR	-	C.H = 2500
	계 단 실	-	시멘트 몰탈	THK30 화강석울갈기	시멘트 몰탈	세라민페인트	-	시멘트 몰탈	조합페인트	-	시멘트 몰탈	조합페인트	-	-	
	사 무 소	-	제물치장 콘크리트	THK3 디렉스타일 (450X450)	시멘트 몰탈	세라민페인트	-	시멘트 몰탈	수성 페인트	-	경량철골 천정을 + THK9.5 석고보드	THK6 아스텍스	M-BAR	-	C.H = 2500
	화 장 실	-	액체방수 1종	바닥타일(300X300)	-	-	-	액체방수 1종(H=1500)	벽타일(300X300)	-	경량철골 천정을 + THK12.5 내수석고보드	아크릴 페인트	M-BAR	-	C.H = 2300
3 층	복 도	-	시멘트 몰탈	THK30 화강석울갈기	시멘트 몰탈	세라민페인트	-	시멘트 몰탈	조합페인트	-	경량철골 천정을 + THK9.5 석고보드	THK9.5 MDF위 조합페인트	M-BAR	-	C.H = 2500
	계 단 실	-	시멘트 몰탈	THK30 화강석울갈기	시멘트 몰탈	세라민페인트	-	시멘트 몰탈	조합페인트	-	시멘트 몰탈	조합페인트	-	-	
	사 무 소	-	제물치장 콘크리트	THK3 디렉스타일 (450X450)	시멘트 몰탈	세라민페인트	-	시멘트 몰탈	수성 페인트	-	경량철골 천정을 + THK9.5 석고보드	THK6 아스텍스	M-BAR	-	C.H = 2500
	화 장 실	-	액체방수 1종	바닥타일(300X300)	-	-	-	액체방수 1종(H=1500)	벽타일(300X300)	-	경량철골 천정을 + THK12.5 내수석고보드	아크릴 페인트	M-BAR	-	C.H = 2300
지 붕	액체방수 1종 + THK20 보호몰탈 + 금속기와깔기														
외 벽	THK30 화강석버너(건식) + 적상목마감														

NOTES

이 도면은 고려전산(주)의 프로그램 교육용으로 작성된 도면입니다.

이 도면의 저작권은 고려전산(주)에 있으며 사전 승인 없이 무단전재 및 재배포할 경우, 관련 법령에 의거 제재를 받을 수 있습니다. 또한, 본사의 교육 이외 용도로의 사용을 금합니다.

REV. NO.

DATE

REVISION DESCRIPTION

DRAWN BY

DESIGNED BY

CHECKED BY

CIVIL ENGINEERING

ARCHITECTURAL

STRUCTURAL

MERCHANICAL

ELECTRICAL

APPROVED BY

PROJECT NO.

SCALE

NONE

DATE

DRAWING NO.

A-02


SHEET NO.

BUILDING NAME

PROJECT

DRAWING TITLE

재 료 마 감 표

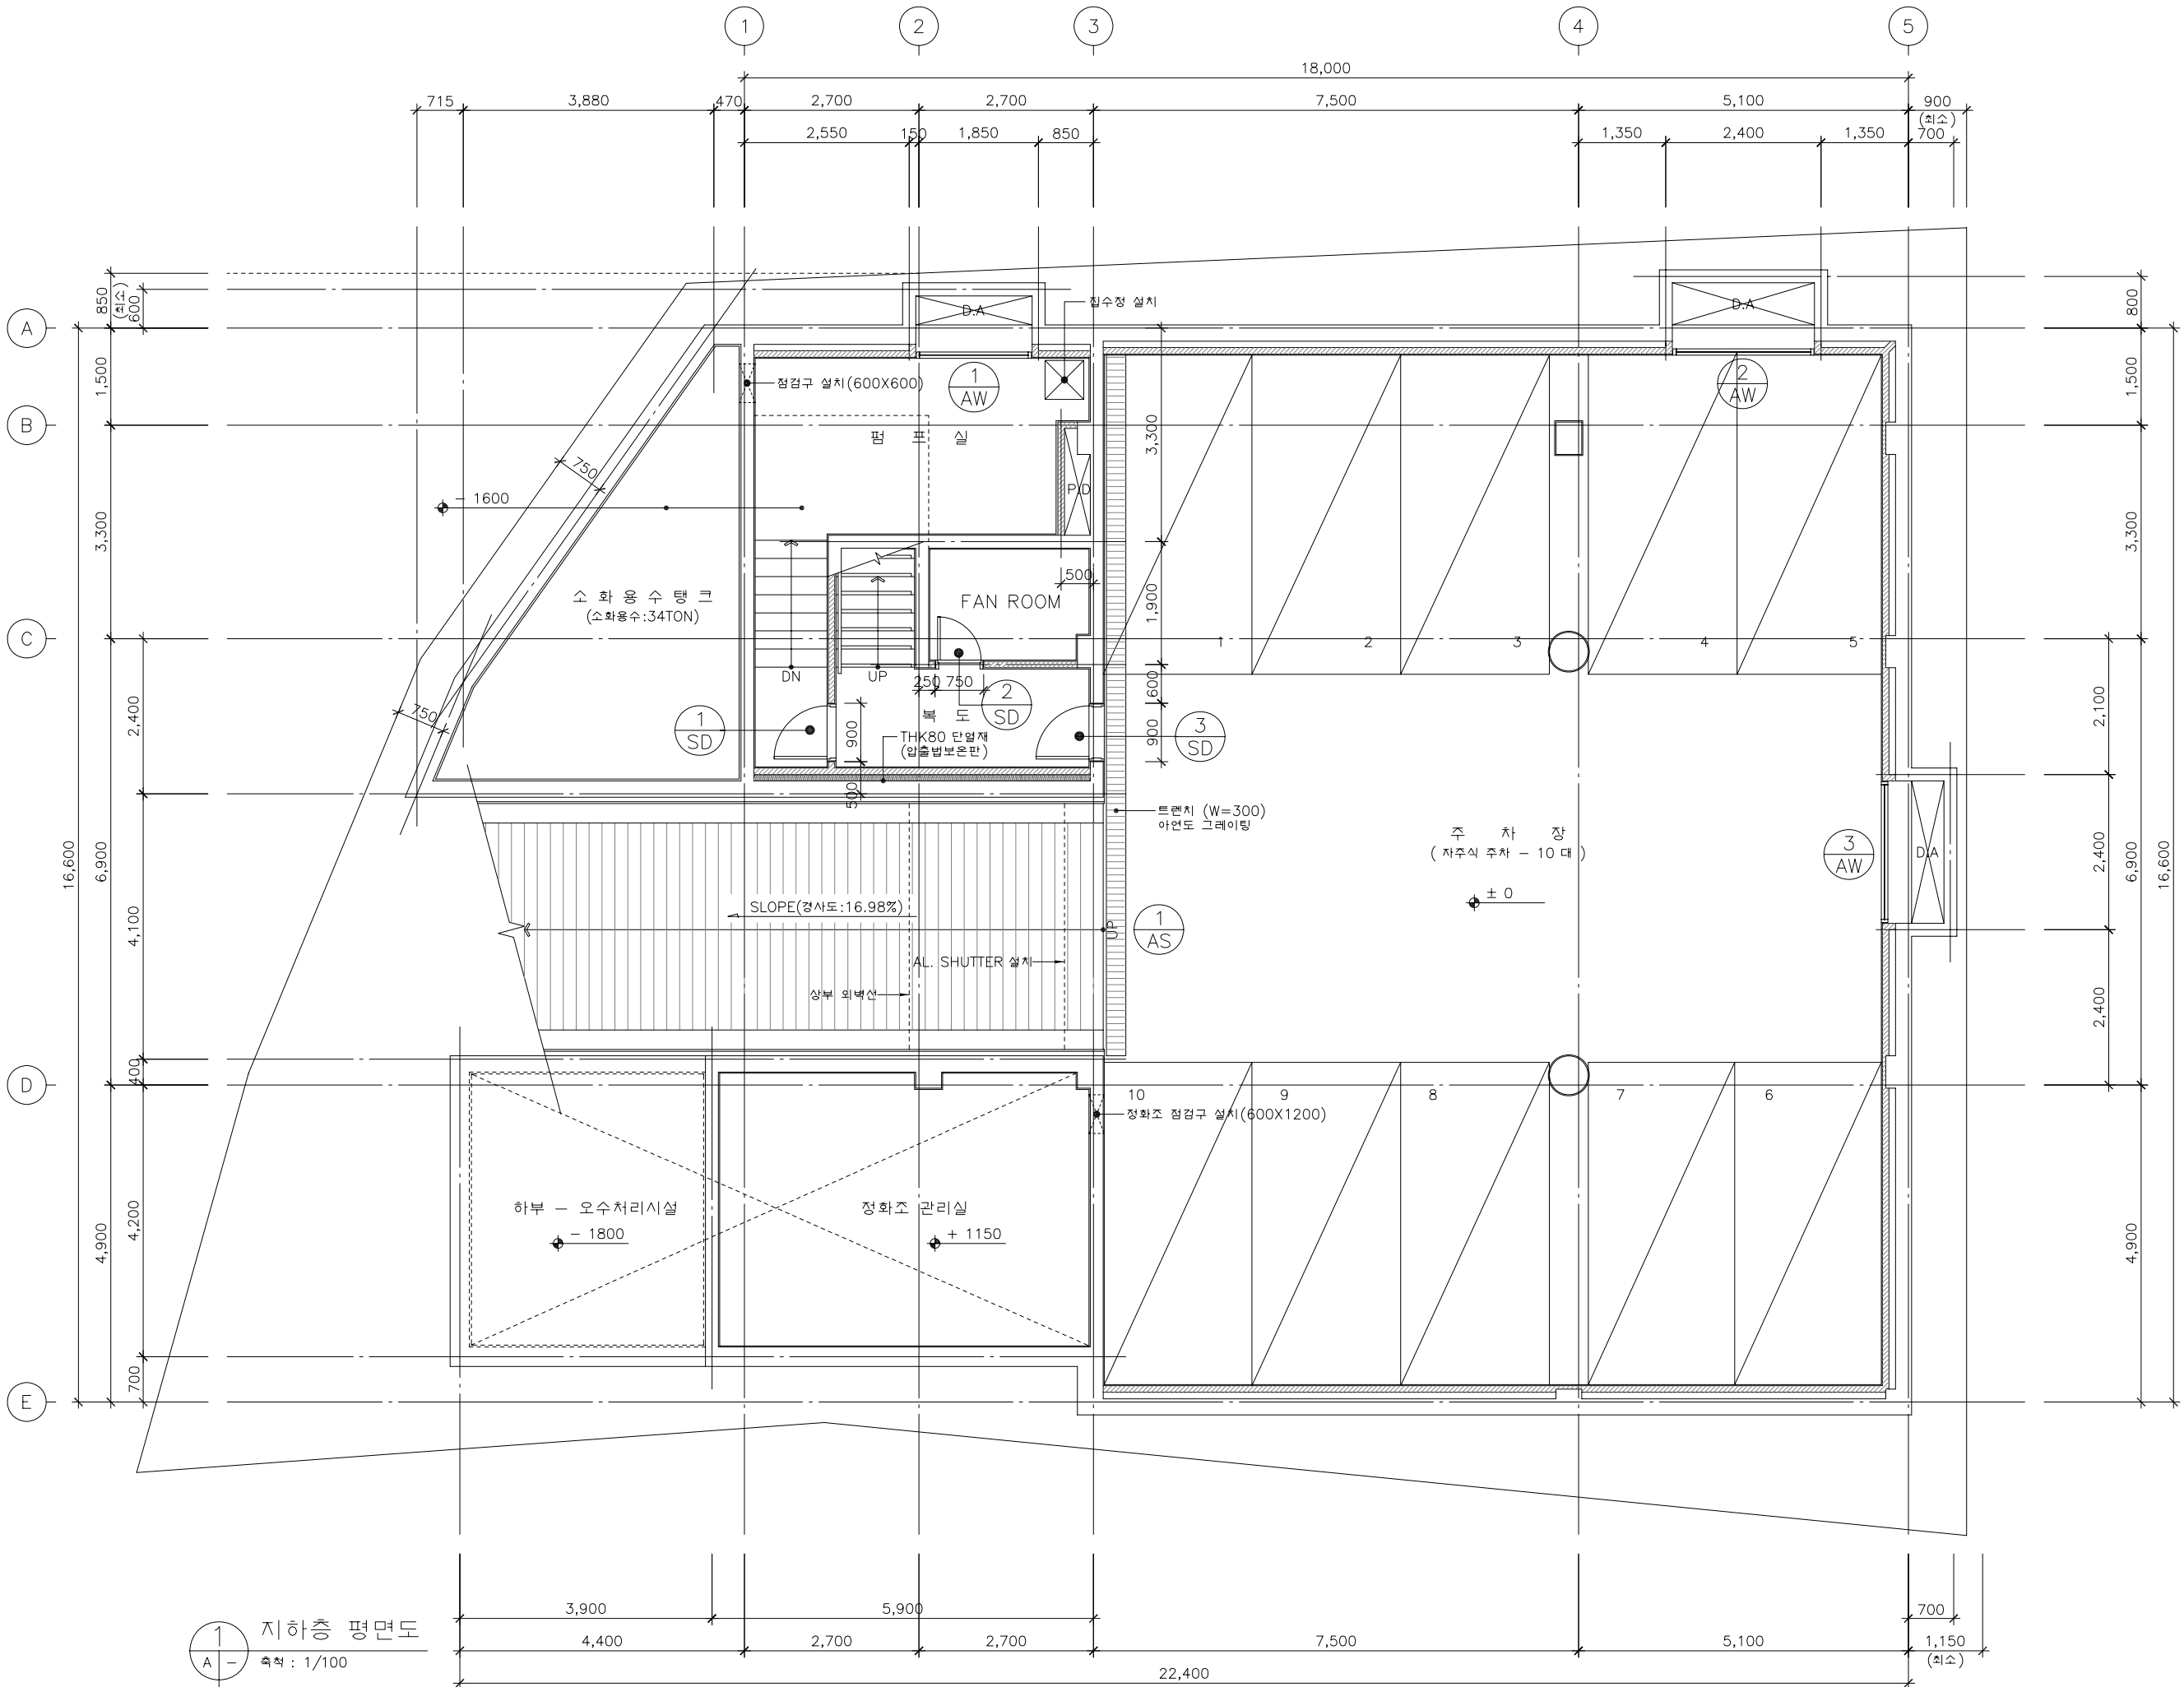

NOTES

이 도면은 고려전산(주)의 프로그램 교육용으로 작성된 도면입니다.

이 도면의 저작권은 고려전산(주)에 있으며 사전 승인 없이 무단전재 및 재배포할 경우, 관련 법령에 의거 제재를 받을 수 있습니다. 또한, 본사의 교육 이외 용도로의 사용을 금합니다.

REV. NO.	DATE	REVISION DESCRIPTION
----------	------	----------------------

DRAWN BY

DESIGNED BY

CHECKED BY

CIVIL ENGINEERING

ARCHITECTURAL

STRUCTURAL

MERCHANICAL

ELECTRICAL

APPROVED BY

PROJECT NO.

SCALE
A1:1/50, A3:1/100

DATE

DRAWING NO.

A-03


SHEET NO.

BUILDING NAME

PROJECT

DRAWING TITLE

지하층 평면도

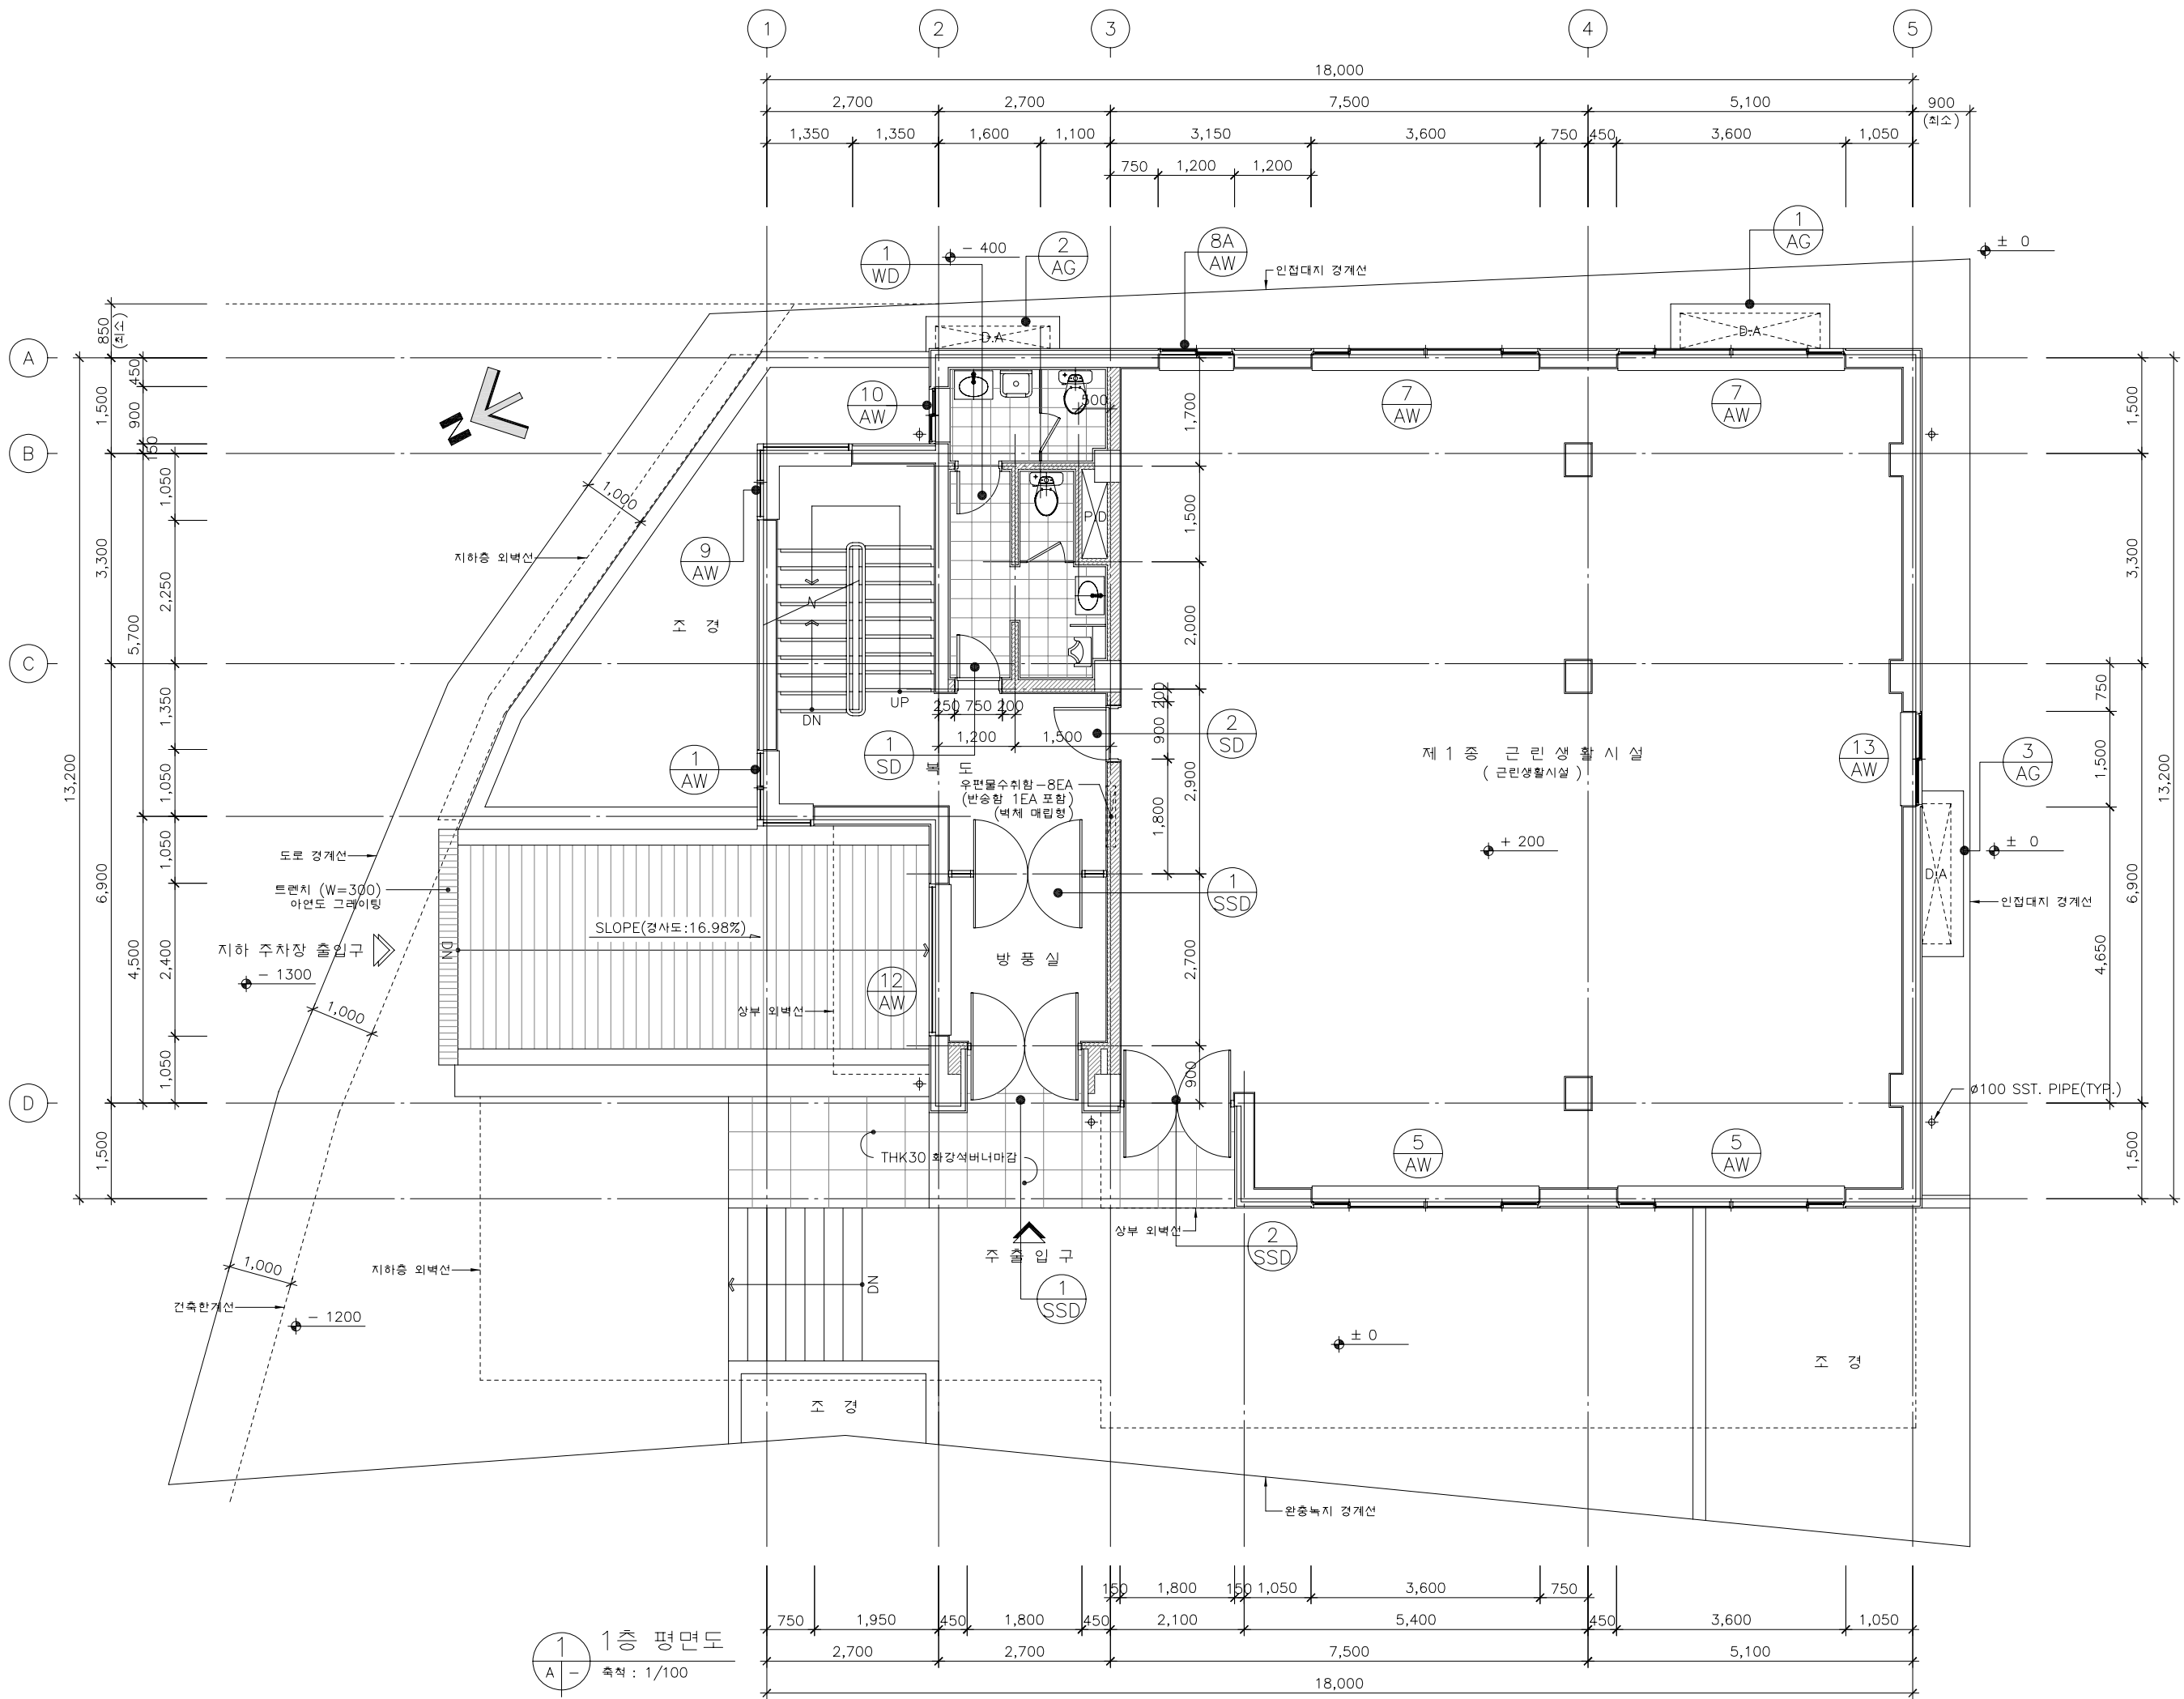


1층 평면도
축척: 1/100

NOTES

이 도면은 고려전산(주)의 프로그램 교육용으로 작성된 도면입니다.

이 도면의 저작권은 고려전산(주)에 있으며 사전 승인 없이 무단전재 및 재배포할 경우, 관련 법령에 의거 제재를 받을 수 있습니다. 또한, 본사의 교육 이외 용도로의 사용을 금합니다.

REV. NO.	DATE	REVISION DESCRIPTION
DRAWN BY		
DESIGNED BY		
CHECKED BY		
CIVIL ENGINEERING		
ARCHITECTURAL		
STRUCTURAL		
MECHANICAL		
ELECTRICAL		
APPROVED BY		
PROJECT NO.		
SCALE A1:1/50, A3:1/100		
DATE		
DRAWING NO. A-04		
SHEET NO.		
BUILDING NAME		
PROJECT		
DRAWING TITLE 1층 평면도		

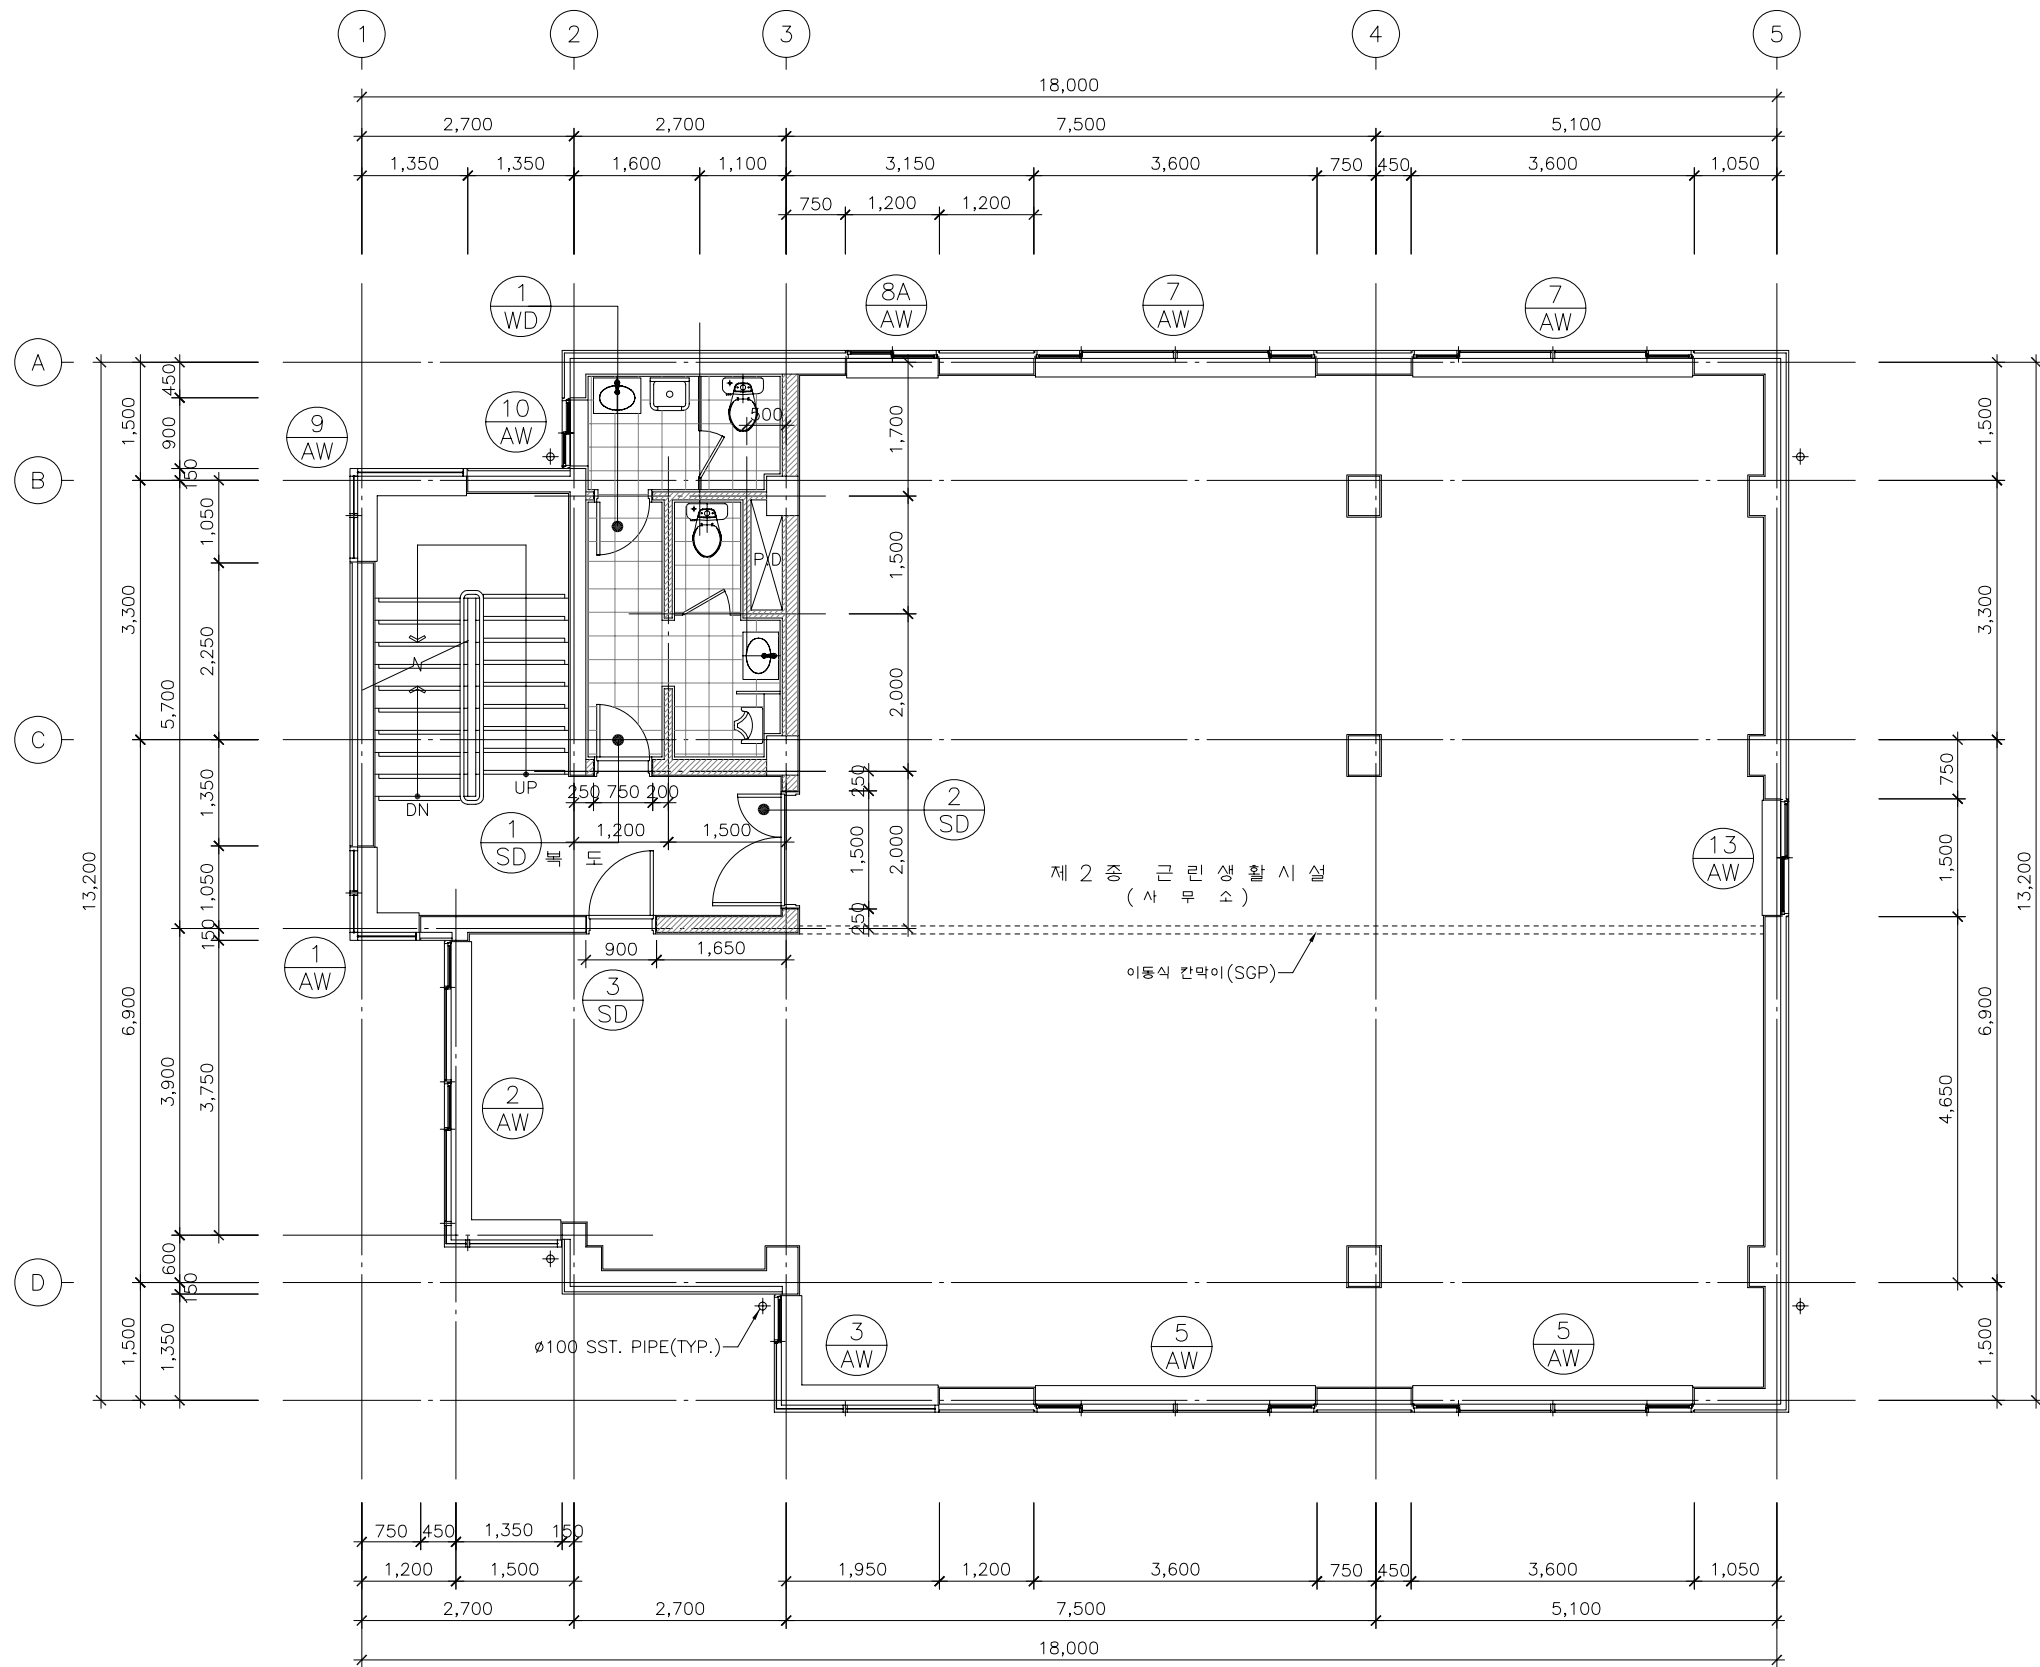

1 2층 평면도
A - 축척 : 1/100

NOTES

이 도면은 고려전산(주)의 프로그램 교육용으로 작성된 도면입니다.

이 도면의 저작권은 고려전산(주)에 있으며 사전 승인 없이 무단전재 및 재배포할 경우, 관련 법령에 의거 제재를 받을 수 있습니다. 또한, 본사의 교육 이외 용도로의 사용을 금합니다.

REV. NO.	DATE	REVISION DESCRIPTION
----------	------	----------------------

DRAWN BY

DESIGNED BY

CHECKED BY

CIVIL ENGINEERING

ARCHITECTURAL

STRUCTURAL

MERCHANICAL

ELECTRICAL

APPROVED BY

PROJECT NO.

SCALE
A1:1/50, A3:1/100

DATE

DRAWING NO.

A-05


SHEET NO.

BUILDING NAME

PROJECT

DRAWING TITLE

2층 평면도

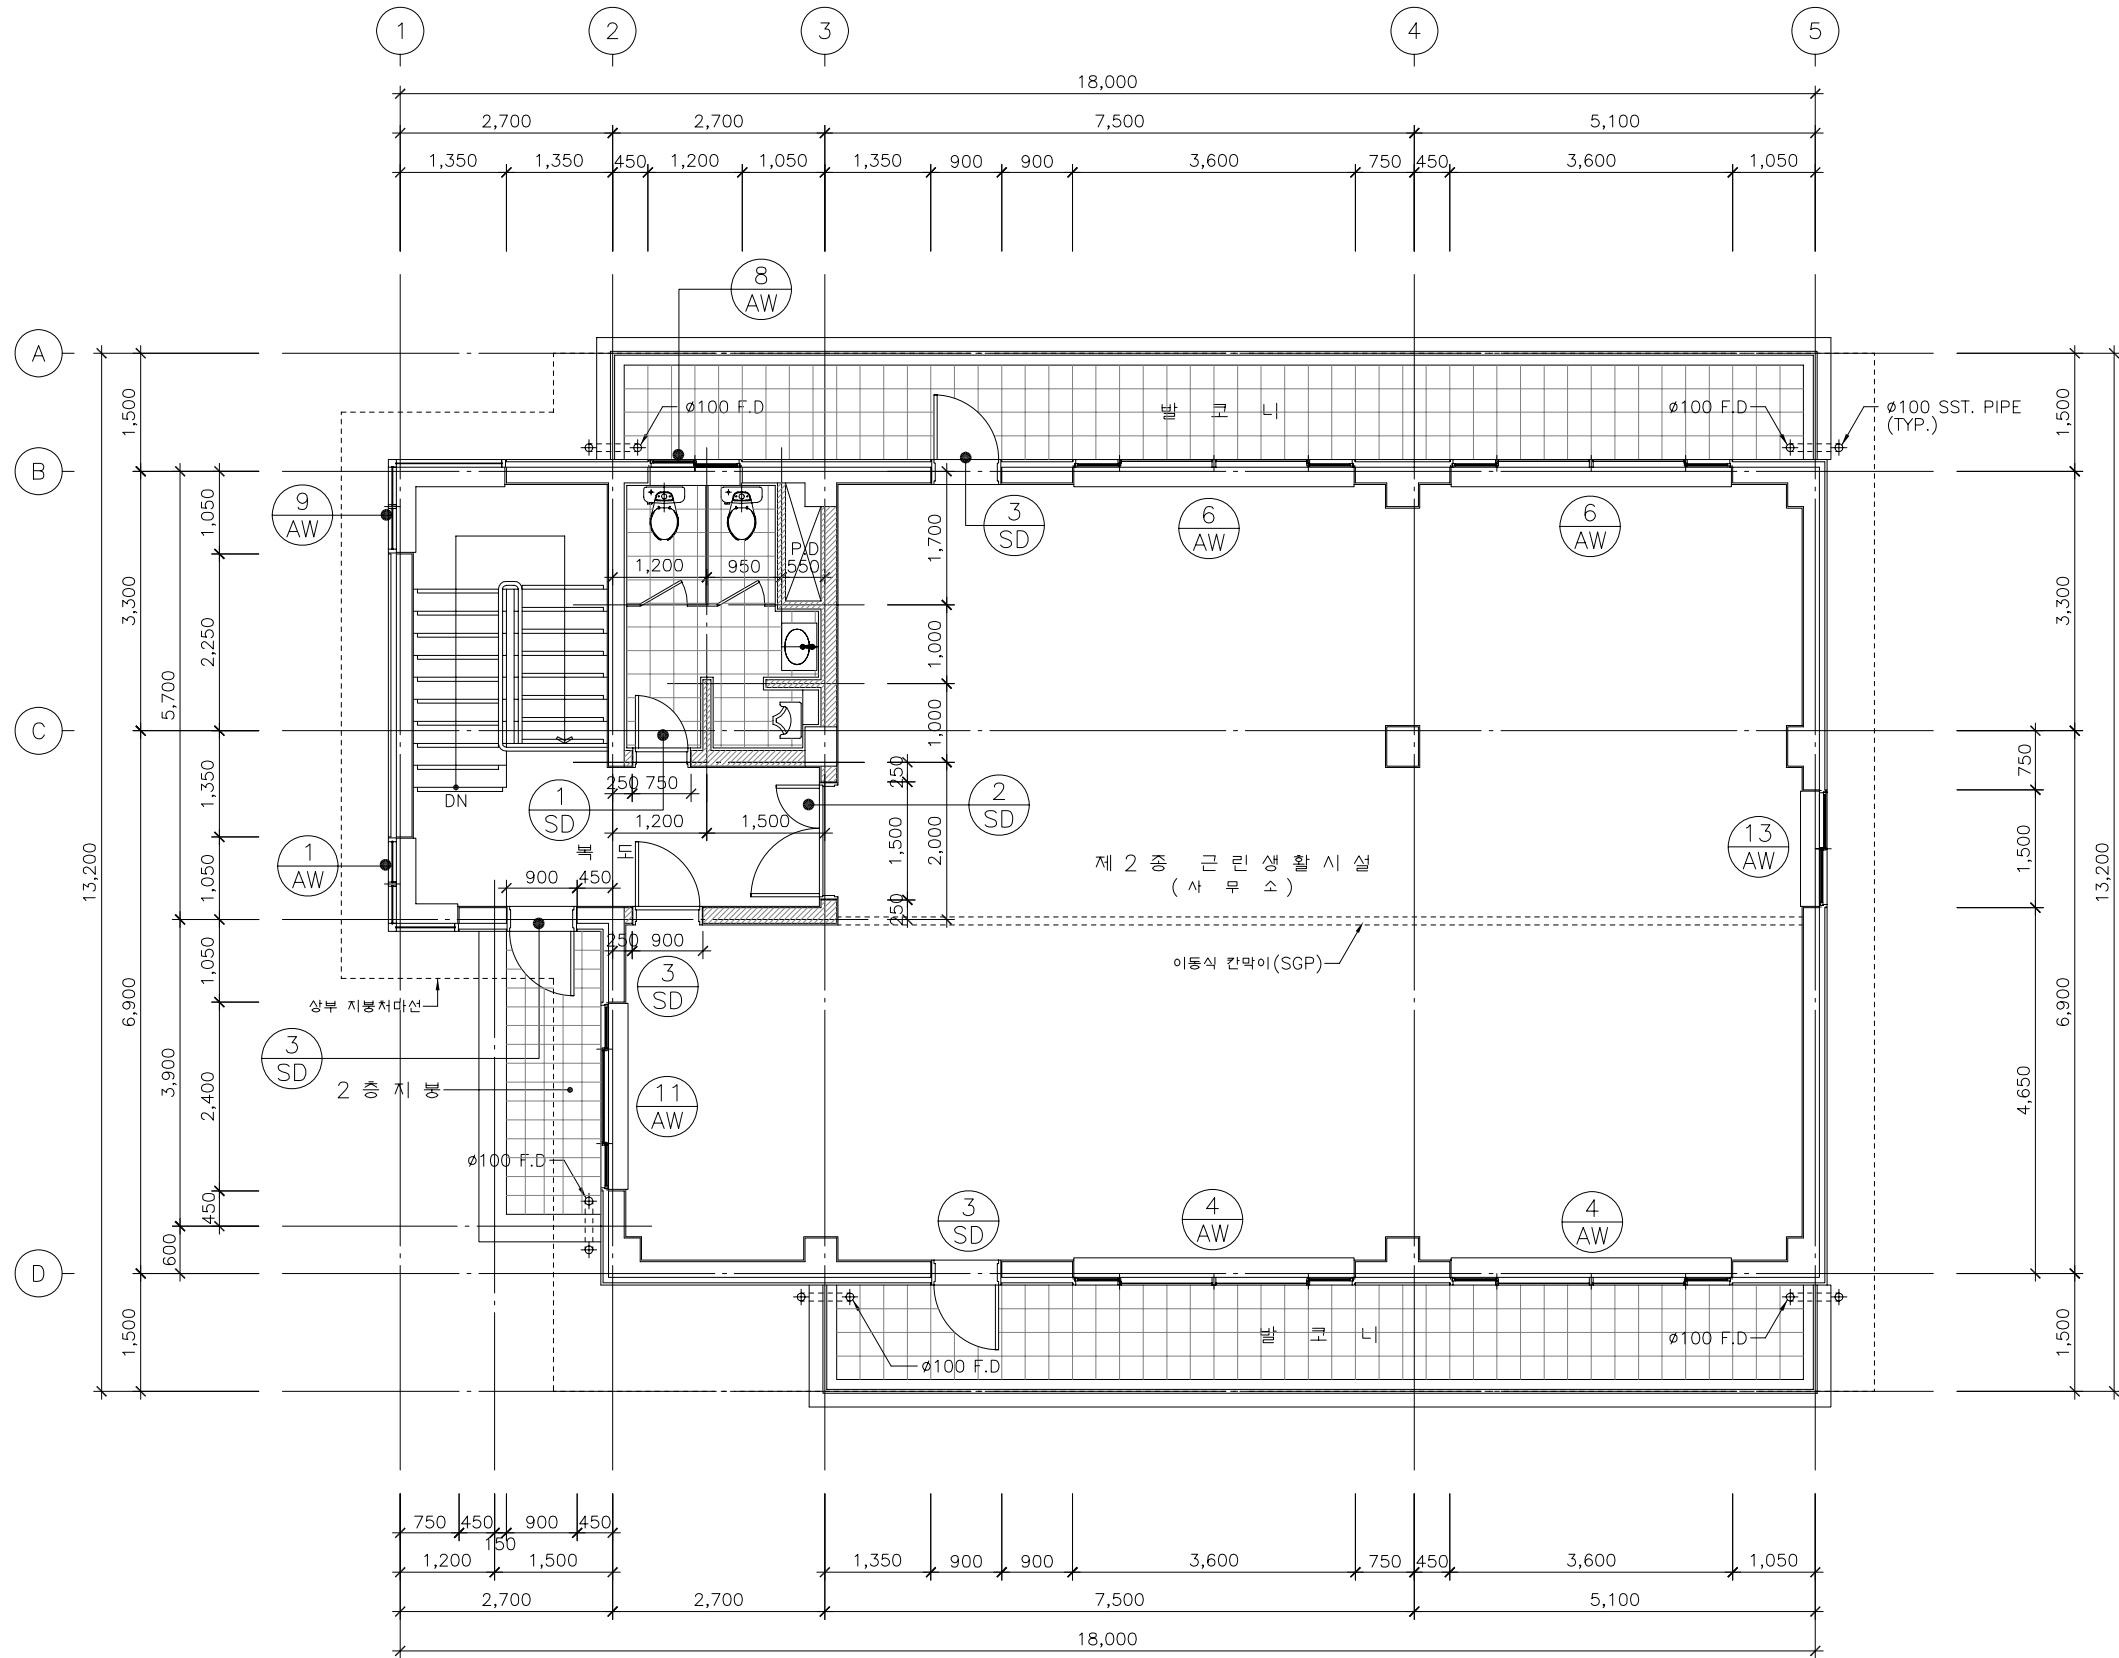

1 3층 평면도
축척 : 1/100

NOTES

이 도면은 고려전산(주)의
프로그램 교육용으로 작성
된 도면입니다.

이 도면의 저작권은 고려전
산(주)에 있으며 사전 승인
없이 무단전제 및 재배포할
경우, 관련 법령에 의거 제
재를 받을 수 있습니다.
또한, 본사의 교육 이외 용
도로의 사용을 금합니다.

REV. NO.	DATE	REVISION DESCRIPTION
-------------	------	-------------------------

DRAWN BY

DESIGNED BY

CHECKED BY

CIVIL ENGINEERING

ARCHITECTURAL

STRUCTURAL

MERCHANICAL

ELECTRICAL

APPROVED BY

PROJECT NO.

SCALE
A1:1/50, A3:1/100

DATE

DRAWING NO.

A-06


SHEET NO.

BUILDING NAME

PROJECT

DRAWING TITLE

3층 평면도

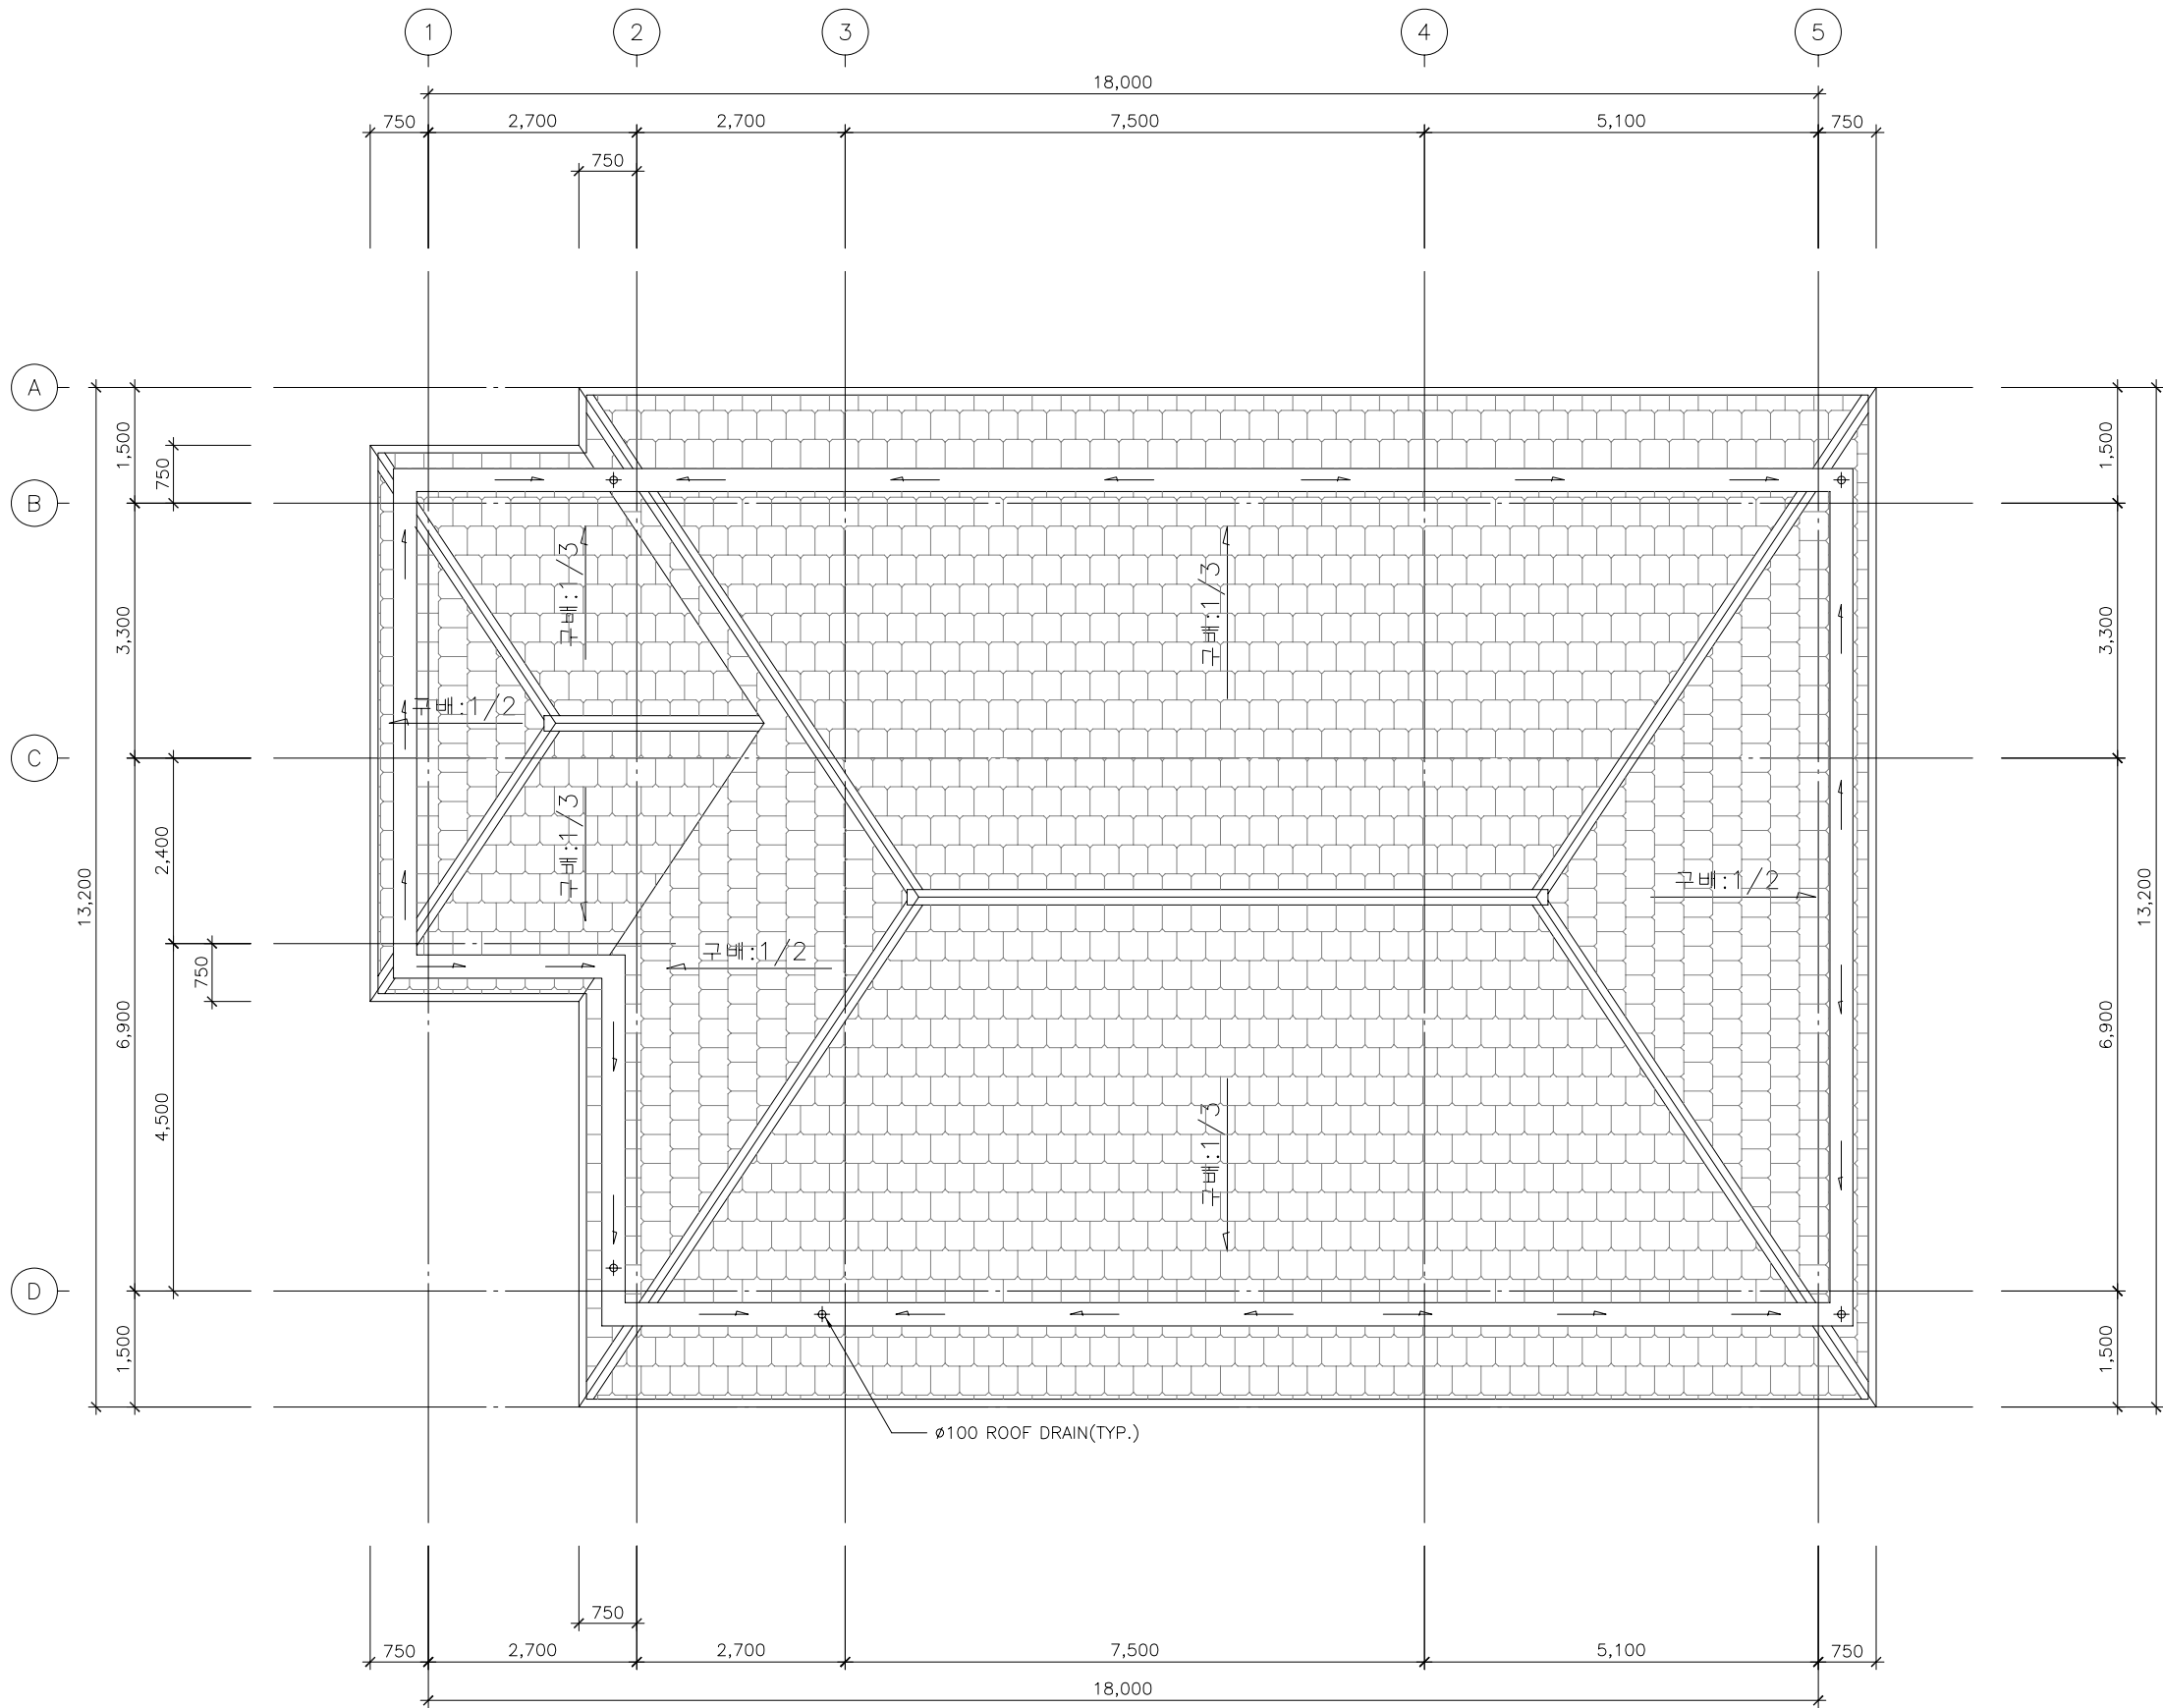

1 지붕 평면도
축척 : 1/100

NOTES

이 도면은 고려전산(주)의
프로그램 교육용으로 작성
된 도면입니다.

이 도면의 저작권은 고려전
산(주)에 있으며 사전 승인
없이 무단전재 및 재배포할
경우, 관련 법령에 의거 제
재를 받을 수 있습니다.
또한, 본사의 교육 이외 용
도로의 사용을 금합니다.

REV. NO.	DATE	REVISION DESCRIPTION
-------------	------	-------------------------

DRAWN BY

DESIGNED BY

CHECKED BY

CIVIL ENGINEERING

ARCHITECTURAL

STRUCTURAL

MERCHANICAL

ELECTRICAL

APPROVED BY

PROJECT NO.

SCALE
A1:1/50, A3:1/100

DATE

DRAWING NO.

A-07


SHEET NO.

BUILDING NAME

PROJECT

DRAWING TITLE

지붕 평면도

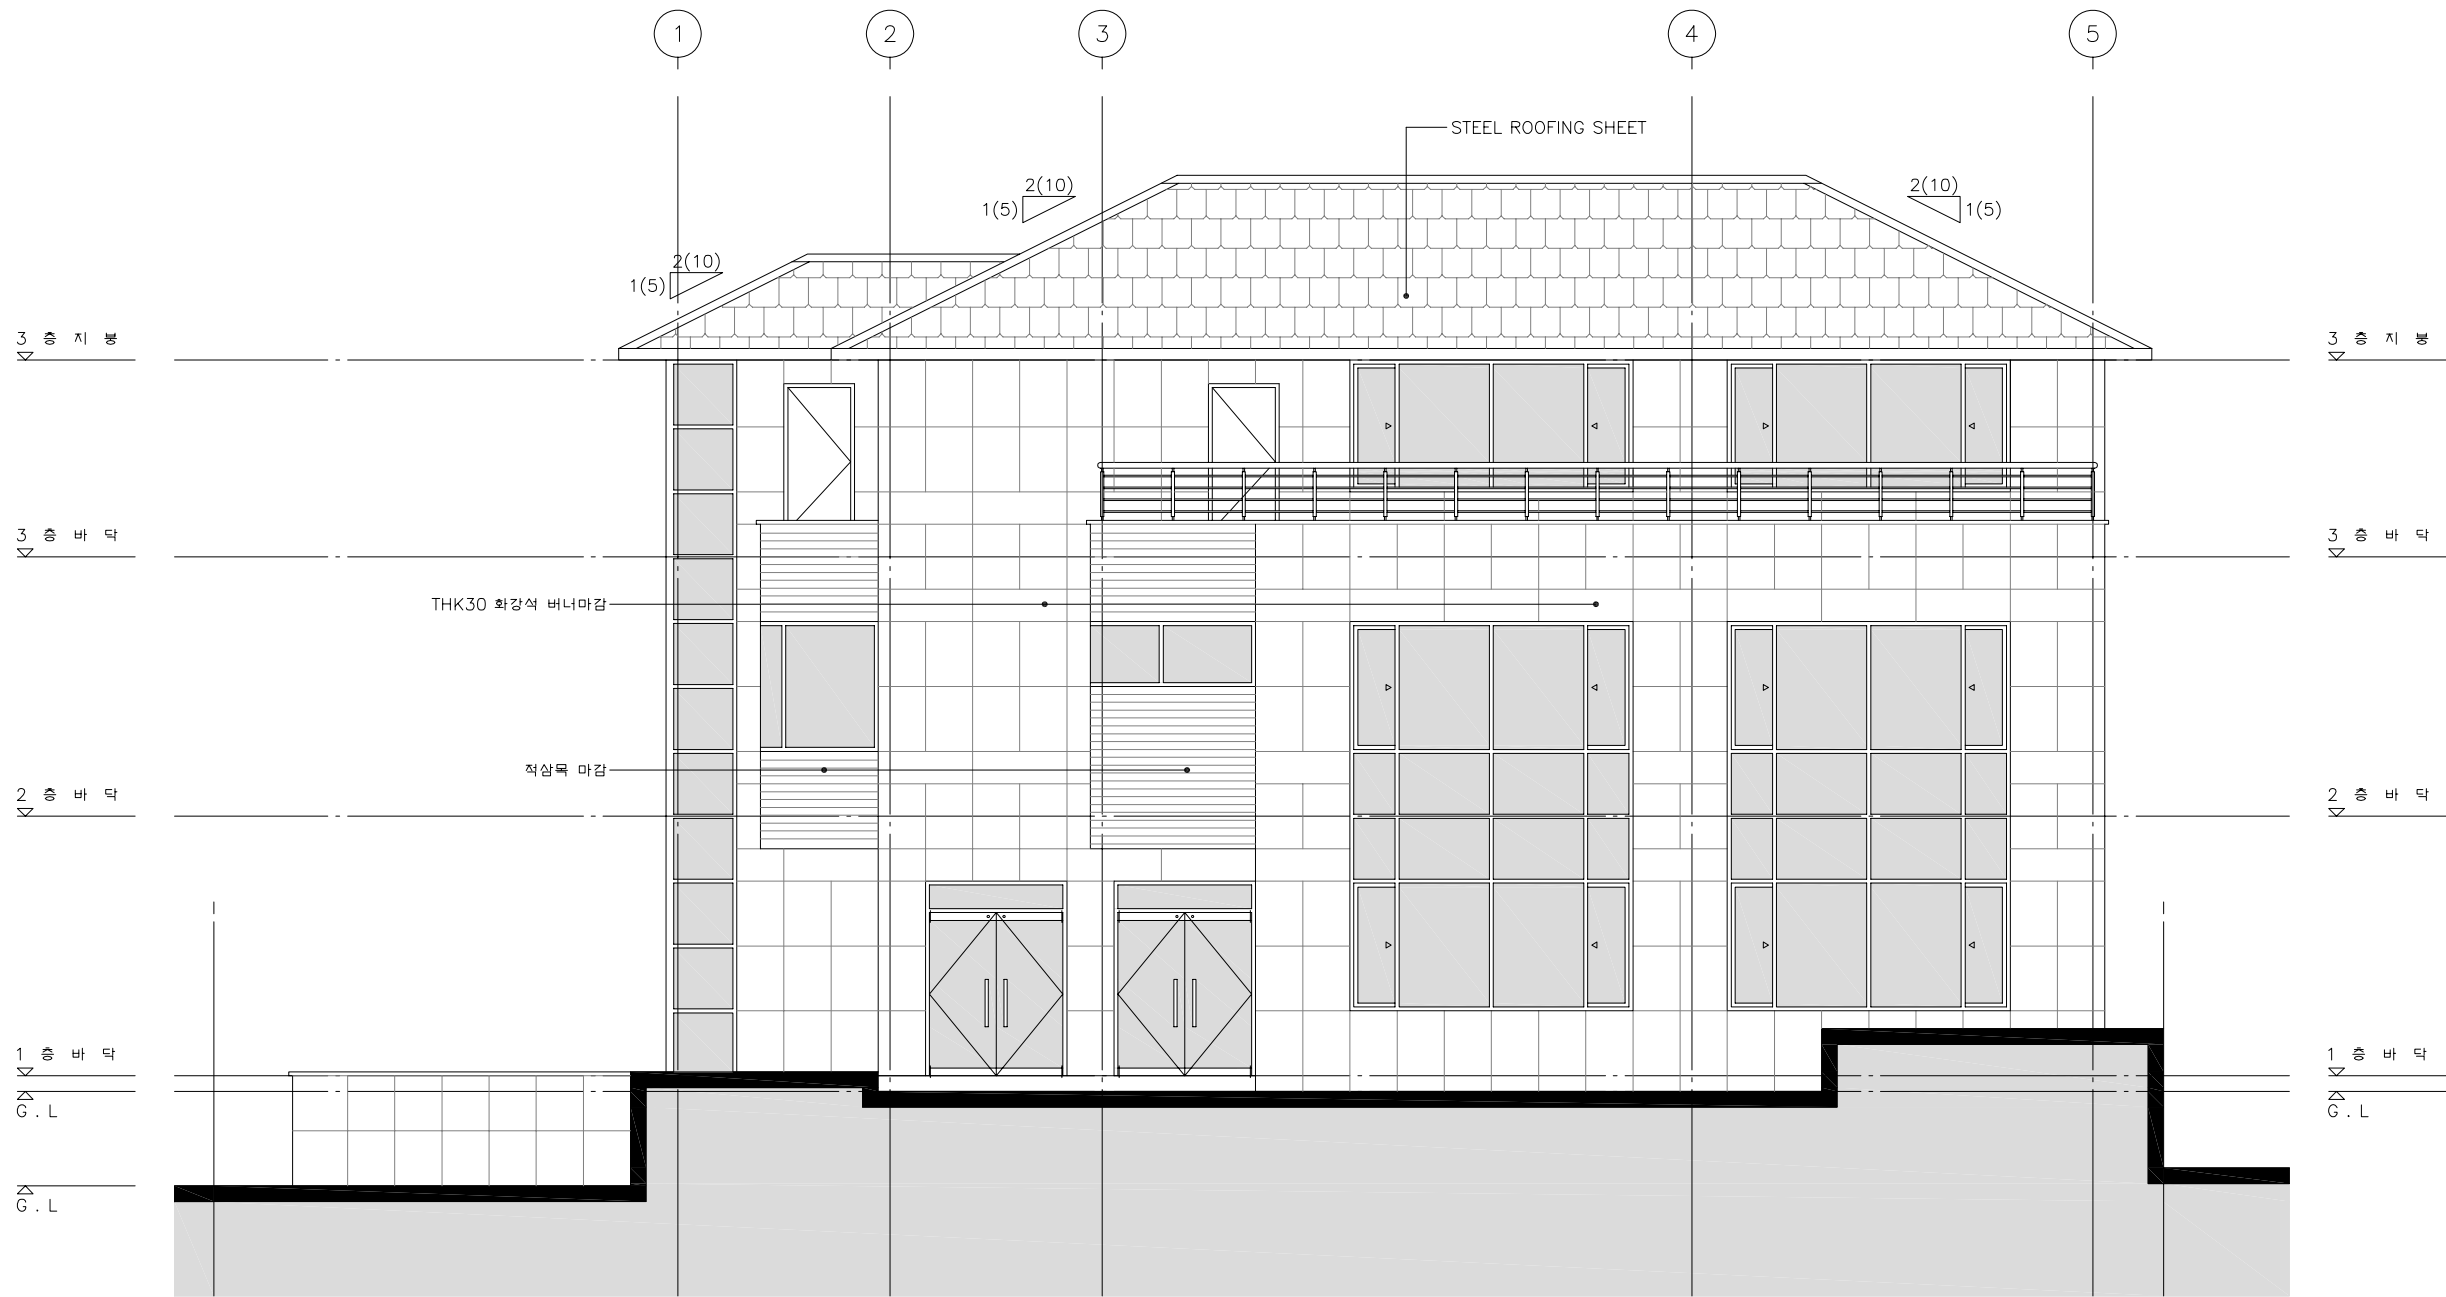

1 정면도
축척 : 1/100

NOTES

이 도면은 고려전산(주)의
프로그램 교육용으로 작성
된 도면입니다.

이 도면의 저작권은 고려전
산(주)에 있으며 사전 승인
없이 무단전재 및 재배포할
경우, 관련 법령에 의거 제
재를 받을 수 있습니다.
또한, 본사의 교육 이외 용
도로의 사용을 금합니다.

REV. NO.	DATE	REVISION DESCRIPTION
----------	------	----------------------

DRAWN BY

DESIGNED BY

CHECKED BY

CIVIL ENGINEERING

ARCHITECTURAL

STRUCTURAL

MERCHANICAL

ELECTRICAL

APPROVED BY

PROJECT NO.

SCALE
A1:1/50, A3:1/100

DATE

DRAWING NO.

A-08

SHEET NO.

BUILDING NAME

PROJECT

DRAWING TITLE

정면도

NOTES

이 도면은 고려전산(주)의
프로그램 교육용으로 작성
된 도면입니다.

이 도면의 저작권은 고려전
산(주)에 있으며 사전 승인
없이 무단전제 및 재배포할
경우, 관련 법령에 의거 제
재를 받을 수 있습니다.
또한, 본사의 교육 이외 용
도로의 사용을 금합니다.

REV. NO.	DATE	REVISION DESCRIPTION
-------------	------	-------------------------

DRAWN BY

DESIGNED BY

CHECKED BY

CIVIL ENGINEERING

ARCHITECTURAL

STRUCTURAL

MERCHANICAL

ELECTRICAL

APPROVED BY

PROJECT NO.

SCALE
A1:1/50, A3:1/100

DATE

DRAWING NO.

A-09


SHEET NO.

BUILDING NAME



PROJECT

DRAWING TITLE

배 면 도

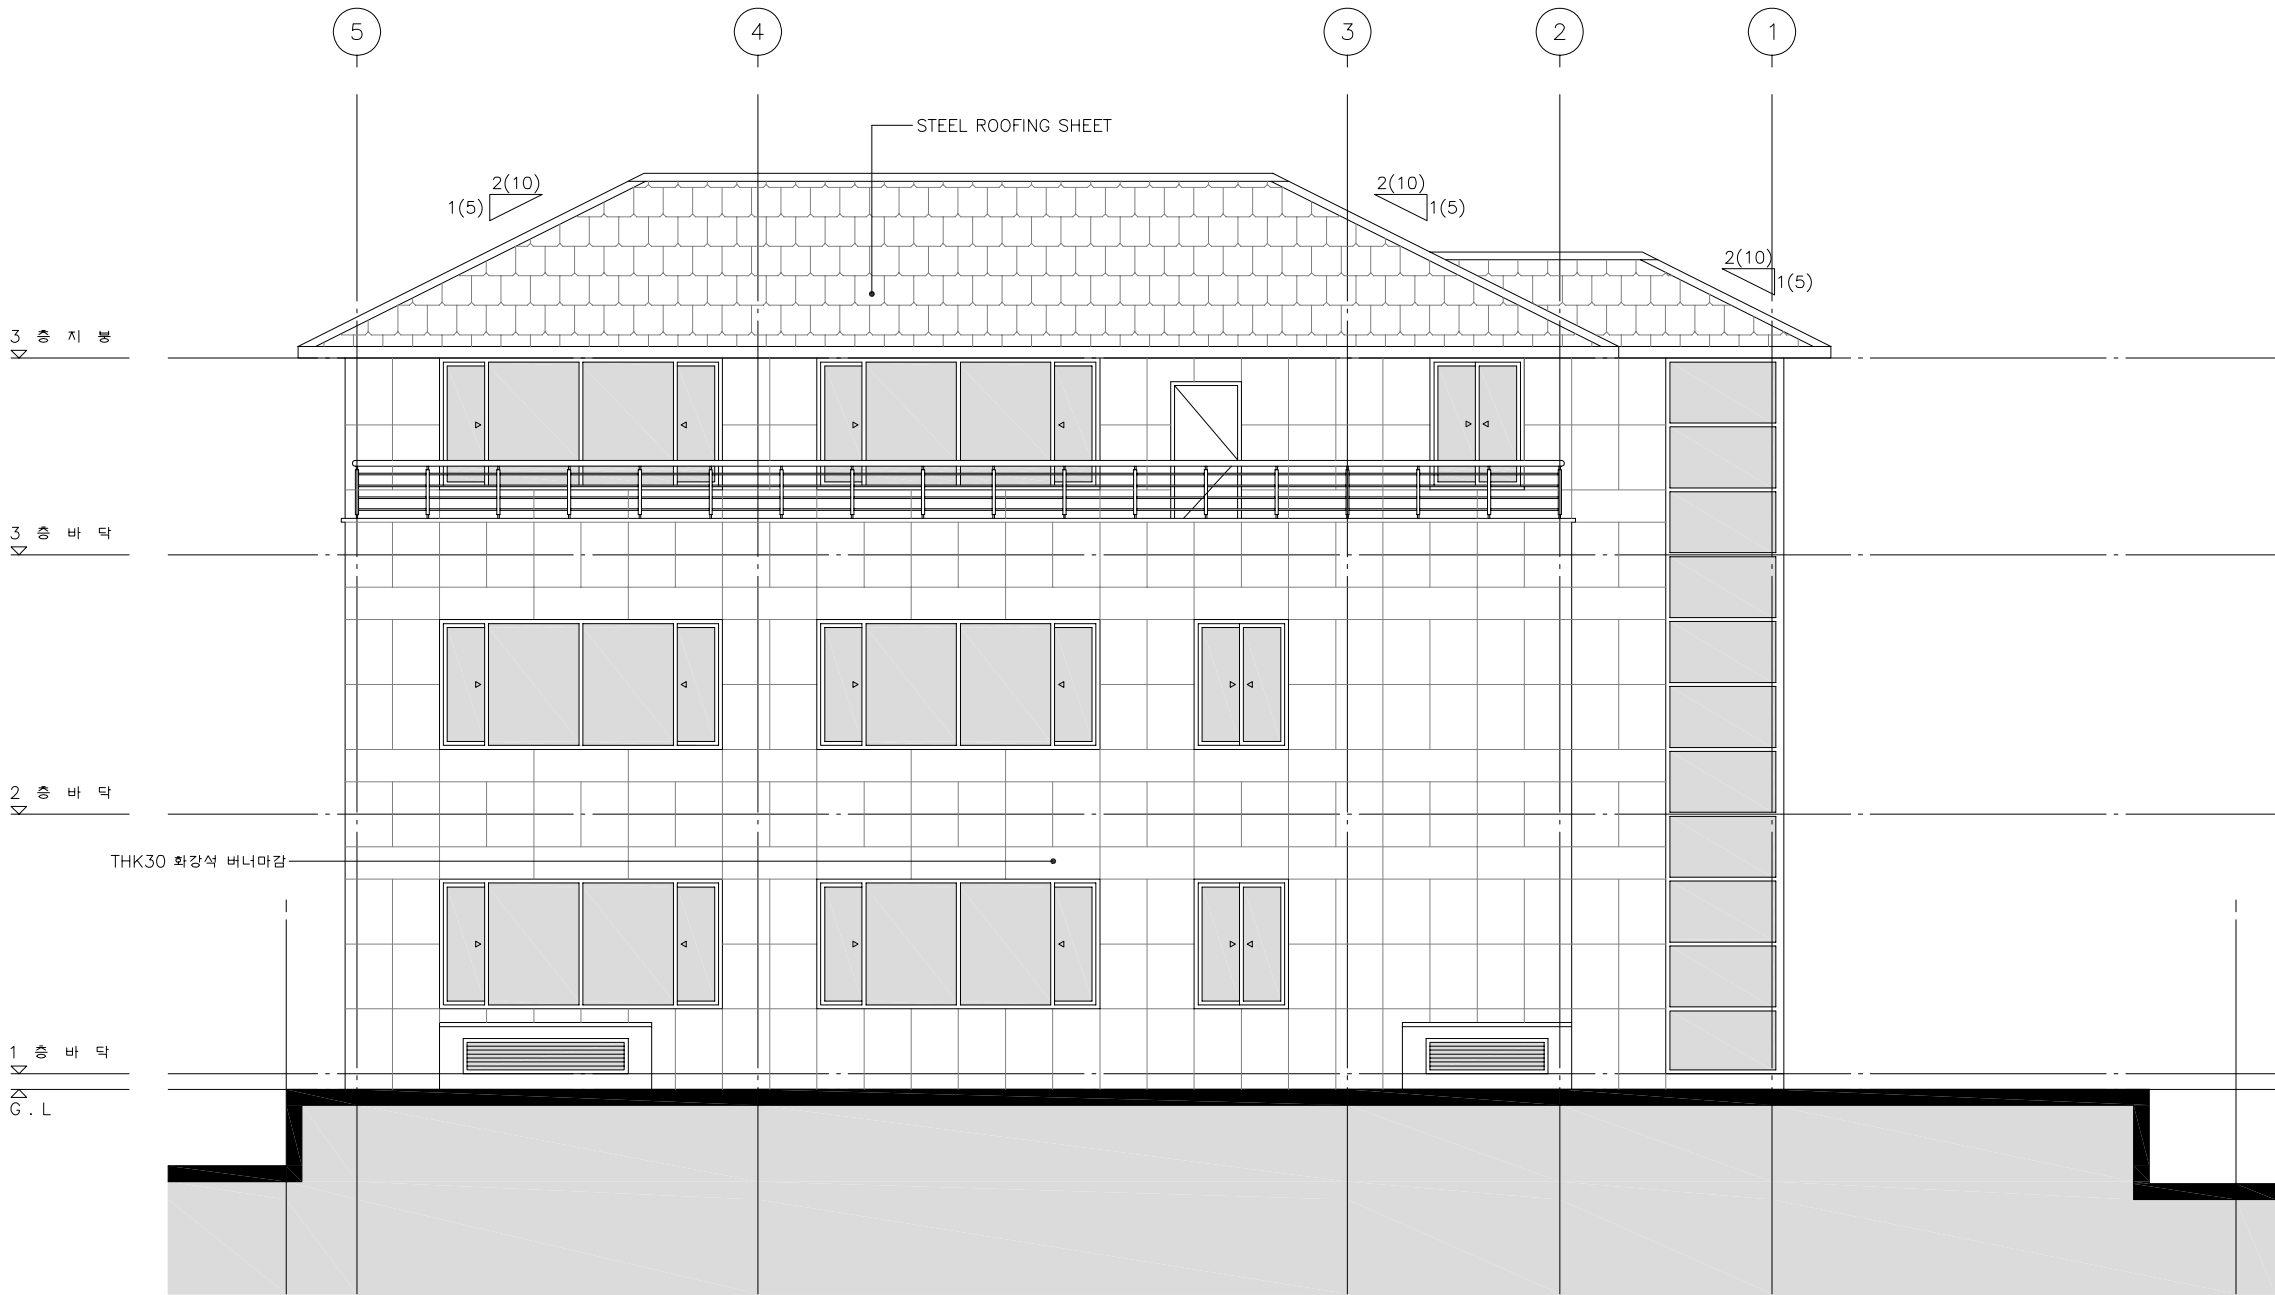

배 면 도
축척 : 1/100

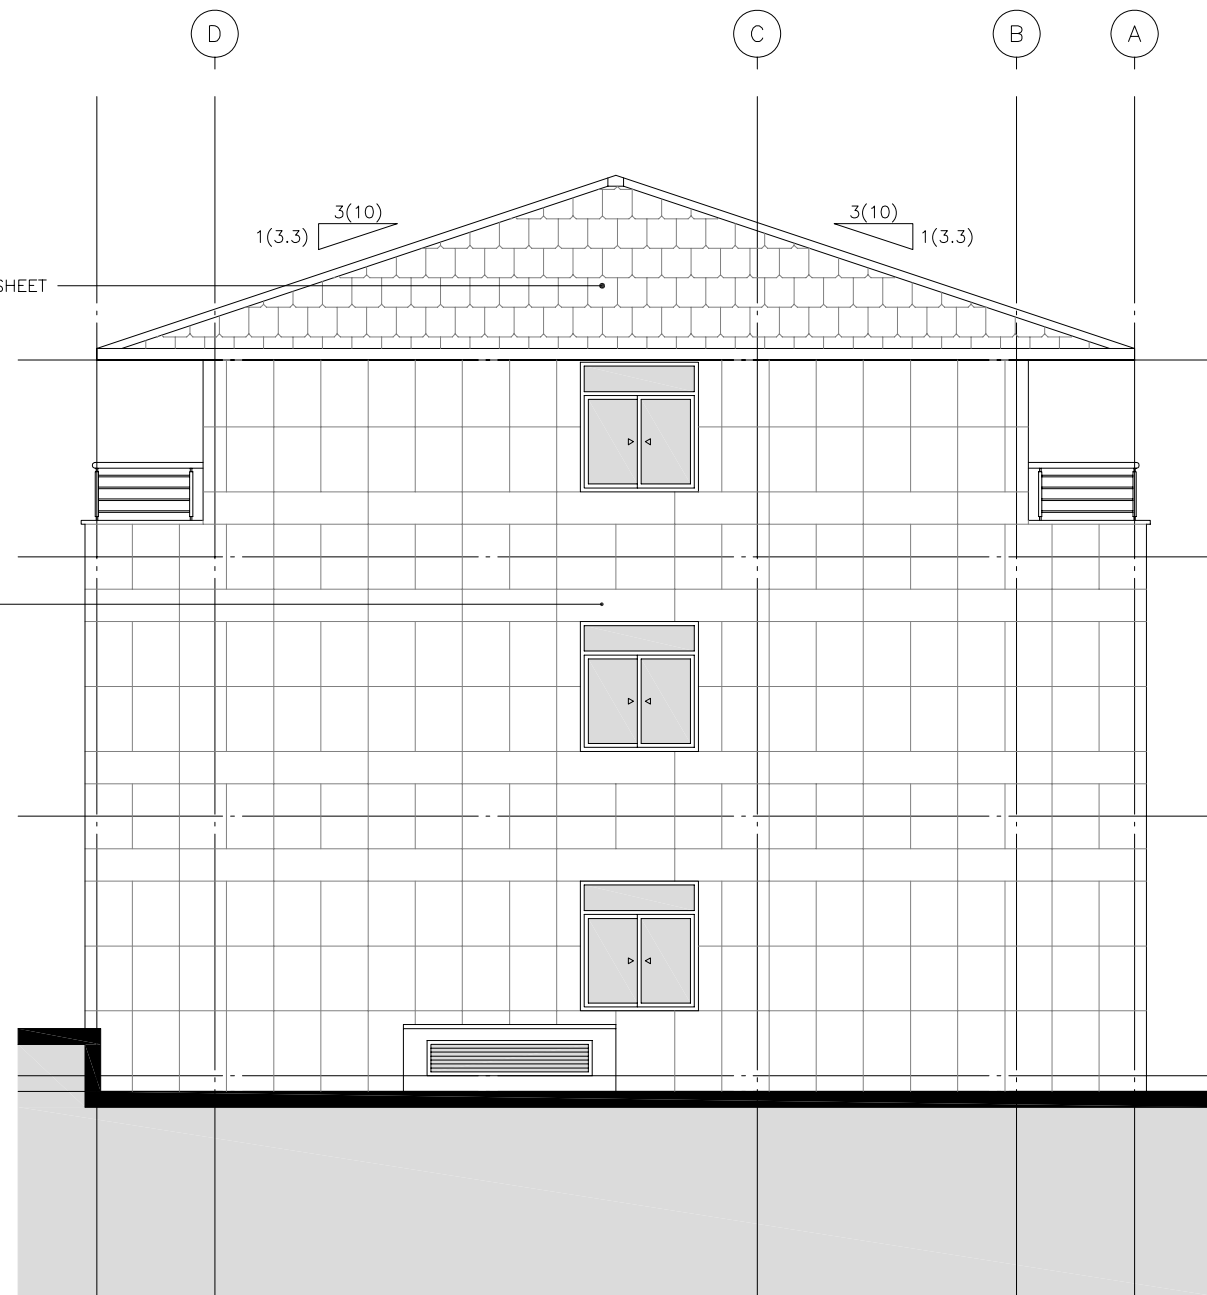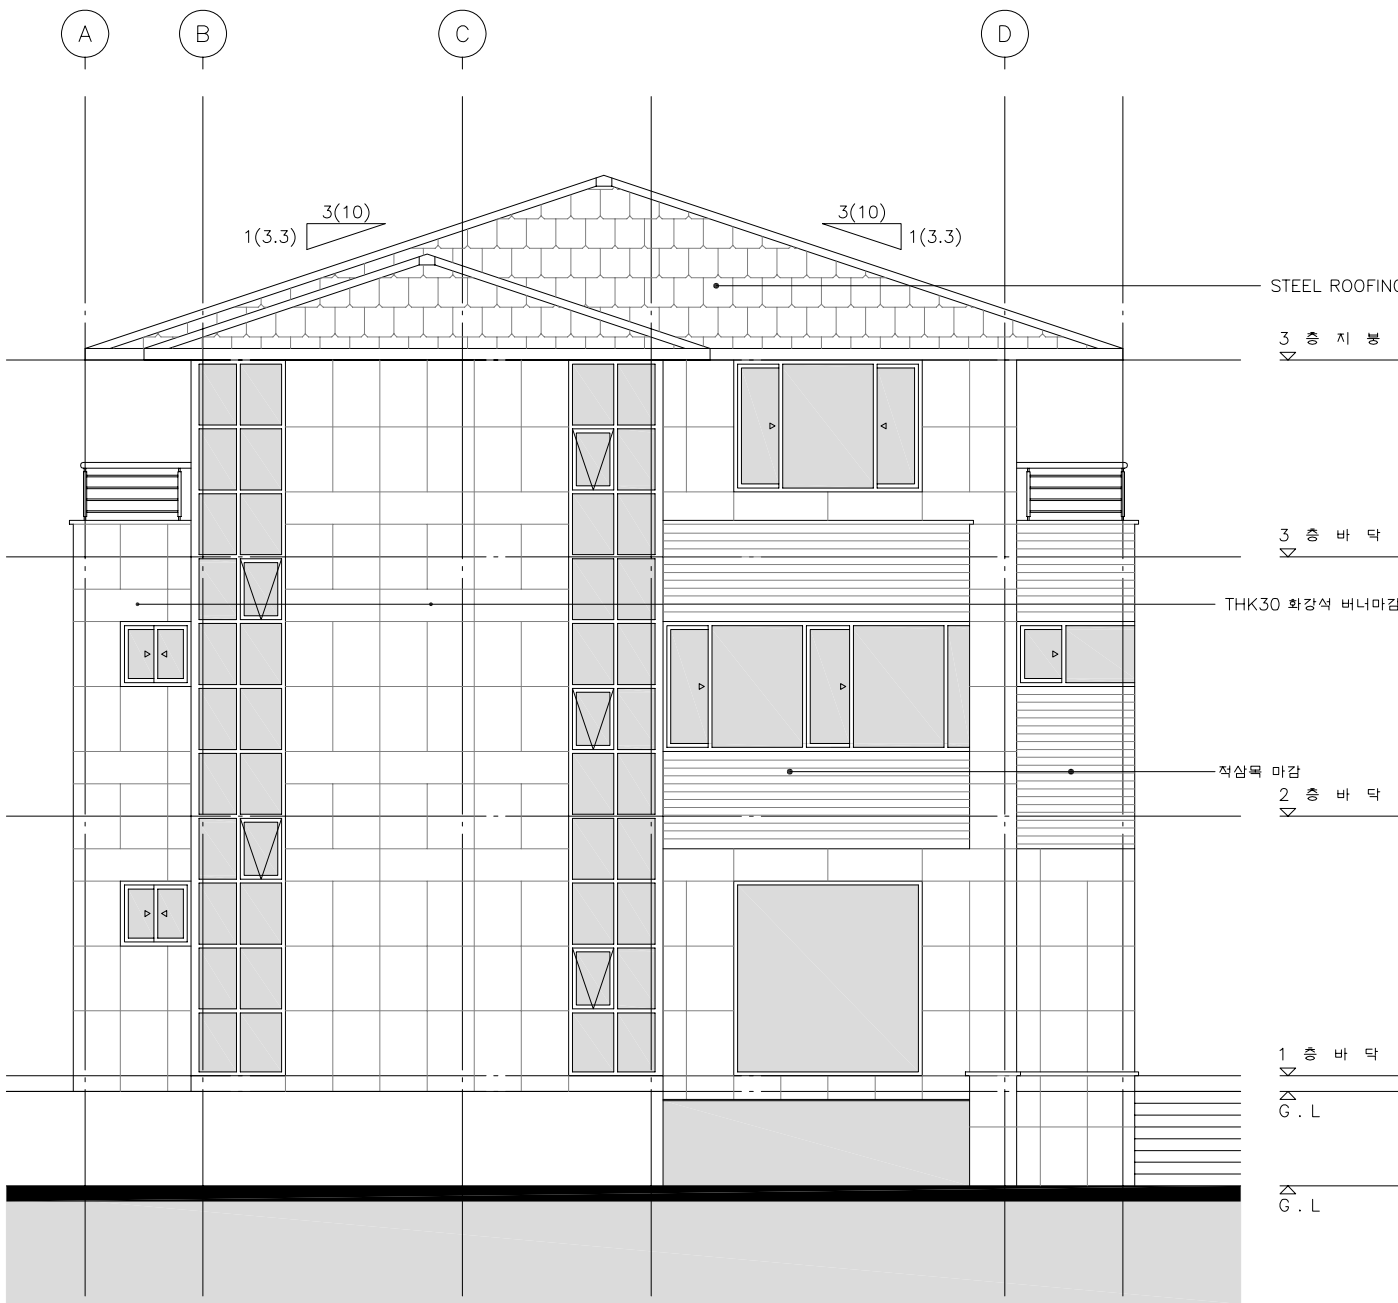

STEEL ROOFING SHEET

3 층 지붕

3 층 바닥

THK30 화강석 버너마감

적삼목 마감
2 층 바닥

1 층 바닥

△
G.L.

△
G.L.

1 좌측면도
축척: 1/100

2 우측면도
축척: 1/100

NOTES

이 도면은 고려전산(주)의
프로그램 교육용으로 작성
된 도면입니다.

이 도면의 저작권은 고려전
산(주)에 있으며 사전 승인
없이 무단전재 및 재배포할
경우, 관련 법령에 의거 제
재를 받을 수 있습니다.
또한, 본사의 교육 이외 용
도로의 사용을 금합니다.

REV. NO.	DATE	REVISION DESCRIPTION
----------	------	----------------------

DRAWN BY

DESIGNED BY

CHECKED BY

CIVIL ENGINEERING

ARCHITECTURAL

STRUCTURAL

MERCHANICAL

ELECTRICAL

APPROVED BY

PROJECT NO.

SCALE
A1:1/50, A3:1/100

DATE

DRAWING NO.
A-10


SHEET NO.

BUILDING NAME

PROJECT

DRAWING TITLE

좌측면도, 우측면도

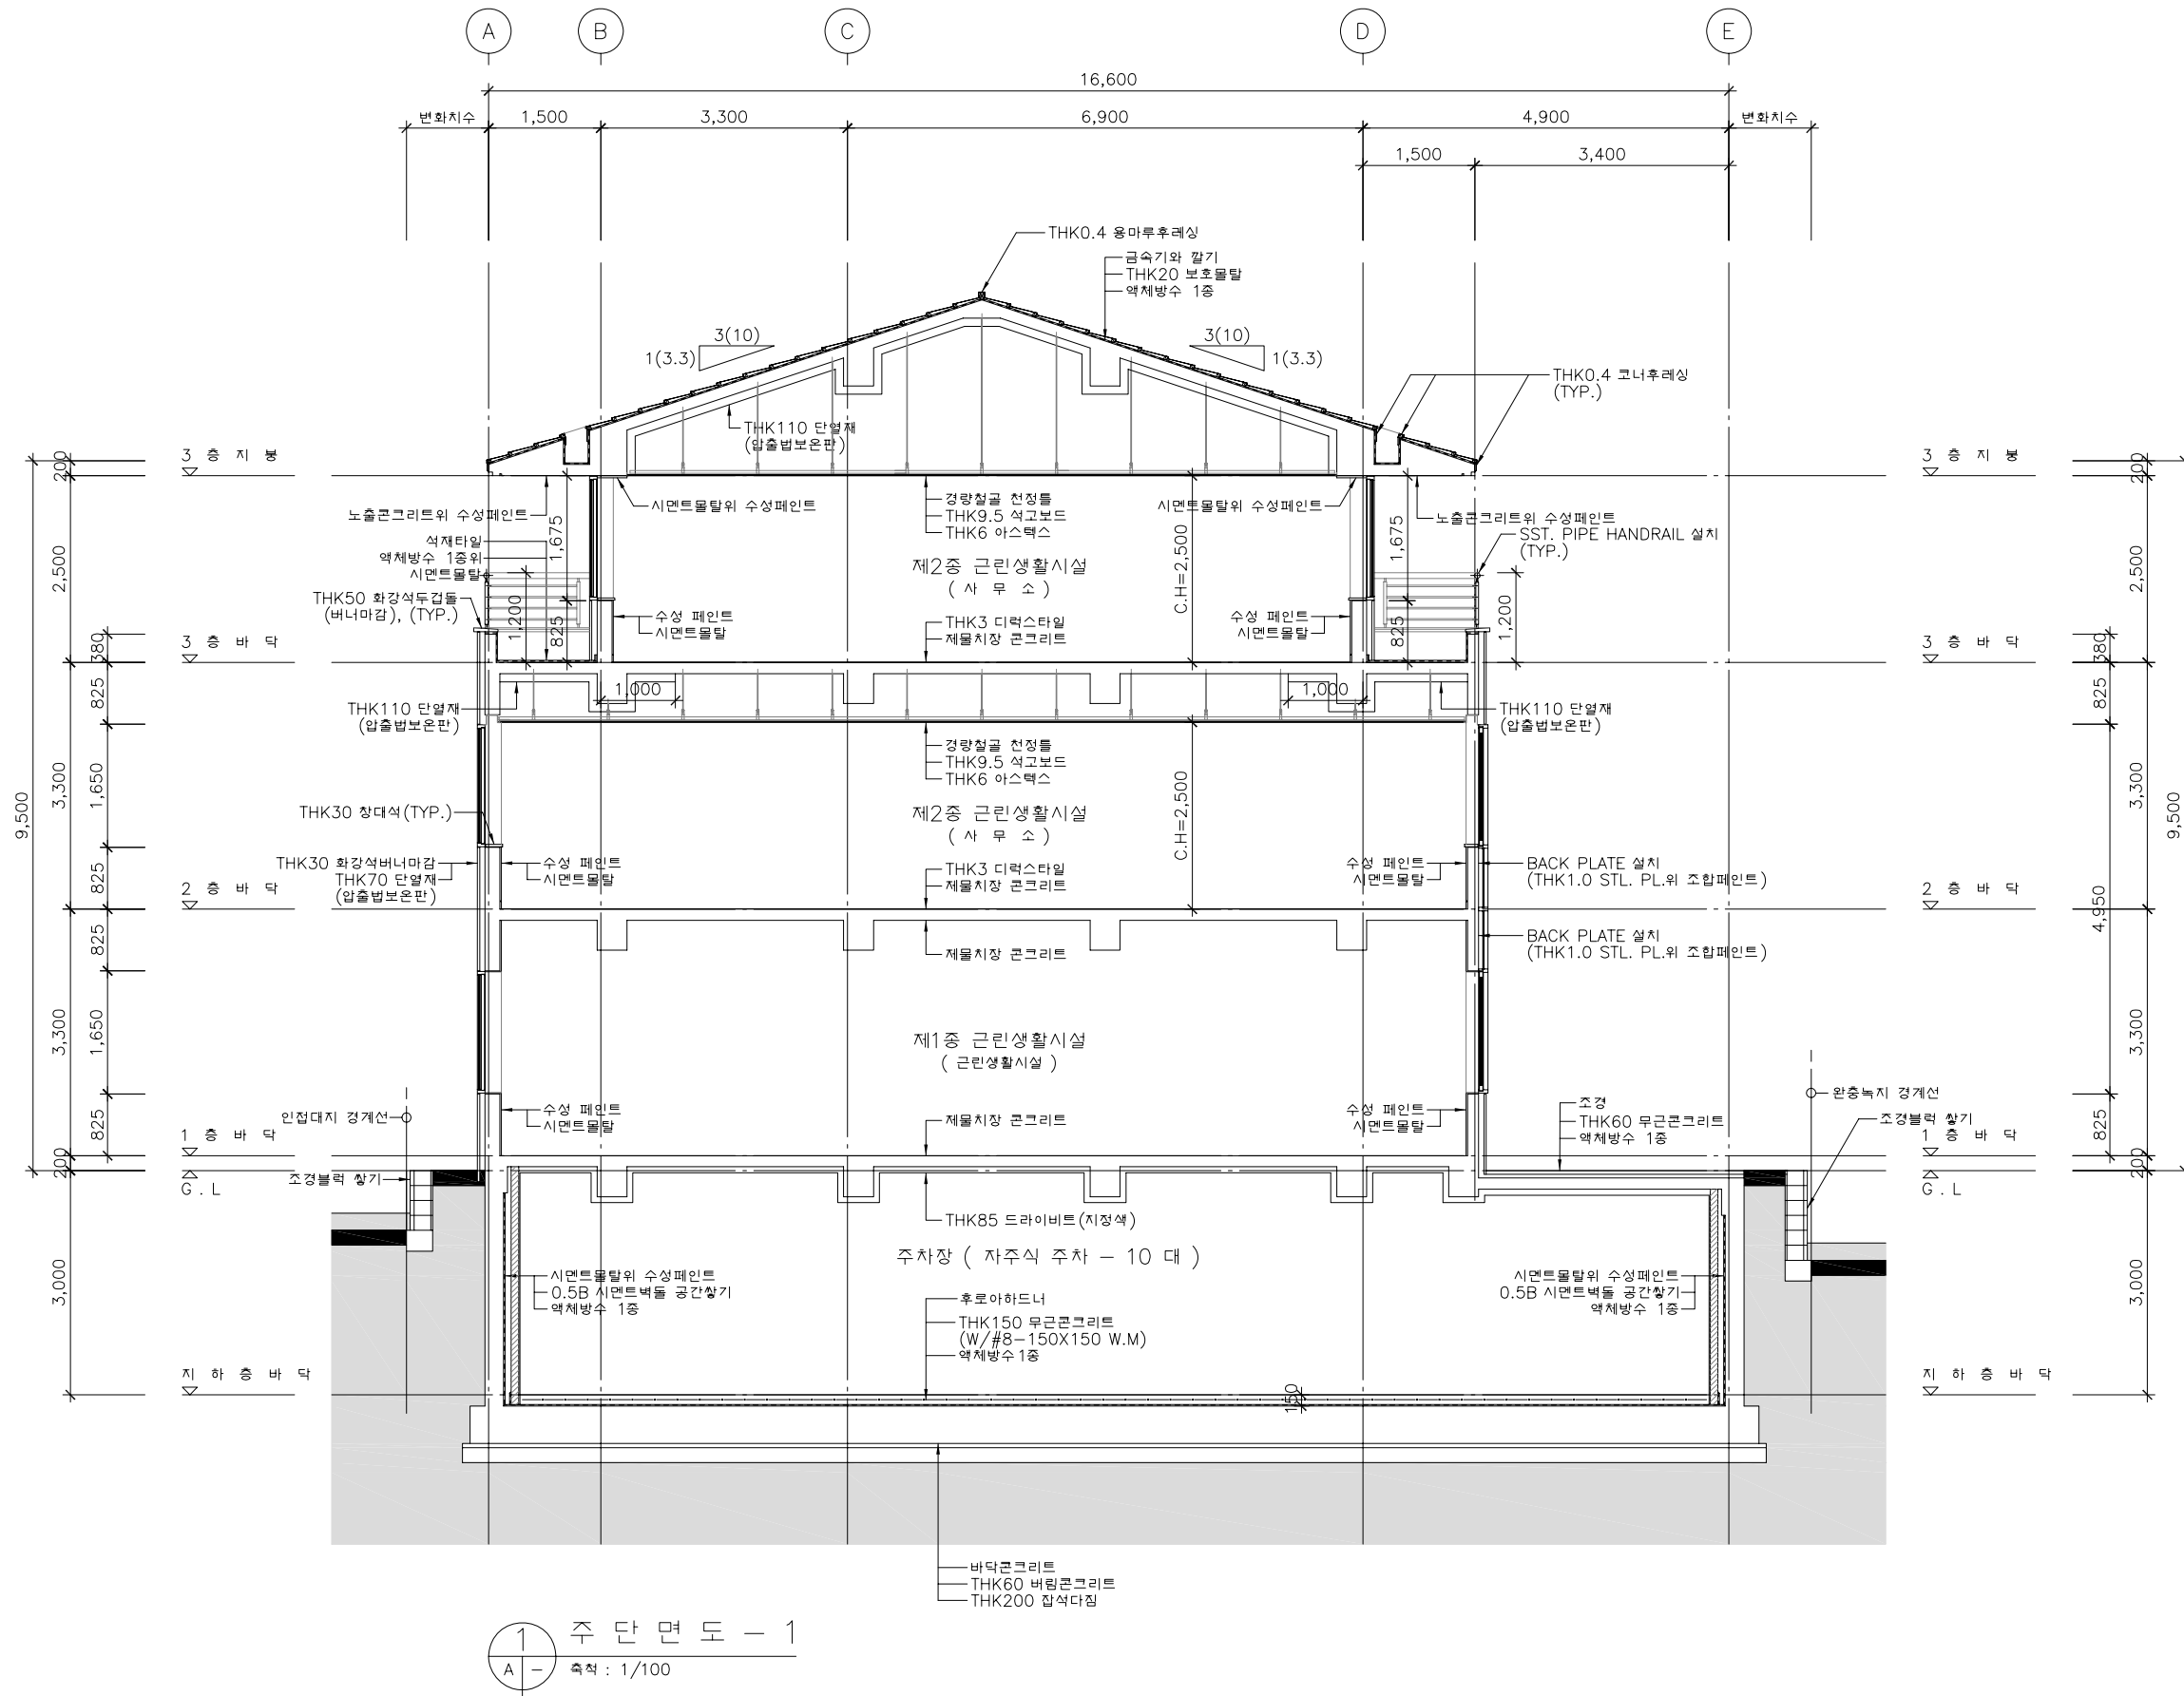

NOTES

이 도면은 고려전산(주)의 프로그램 교육용으로 작성된 도면입니다.

이 도면의 저작권은 고려전산(주)에 있으며 사전 승인 없이 무단전제 및 재배포할 경우, 관련 법령에 의거 제재를 받을 수 있습니다. 또한, 본사의 교육 이외 용도로의 사용을 금합니다.

REV. NO.	DATE	REVISION DESCRIPTION
DRAWN BY		
DESIGNED BY		
CHECKED BY		
CIVIL ENGINEERING		
ARCHITECTURAL		
STRUCTURAL		
MECHANICAL		
ELECTRICAL		
APPROVED BY		
PROJECT NO.		
SCALE A1:1/50, A3:1/100		
DATE		
DRAWING NO. A-11		
SHEET NO.		
BUILDING NAME		
PROJECT		
DRAWING TITLE 주단면도 - 1		

TYPE - 가	TYPE - 나	TYPE - 다	TYPE - 라	TYPE - 마	TYPE - 바	
TYPE - A	TYPE - B	TYPE - C		TYPE - D	TYPE - E	TYPE - F
TYPE - L		TYPE - G	TYPE - H	TYPE - I	TYPE - J	TYPE - K
		TYPE - M				

NOTES		
이 도면은 고려전산(주)의 프로그램 교육용으로 작성된 도면입니다.		
이 도면의 저작권은 고려전산(주)에 있으며 사전 승인 없이 무단전재 및 재배포할 경우, 관련 법령에 의거 제재를 받을 수 있습니다. 또한, 본사의 교육 이외 용도로의 사용을 금합니다.		
REV. NO.	DATE	REVISION DESCRIPTION
DRAWN BY		
DESIGNED BY		
CHECKED BY		
CIVIL ENGINEERING		
ARCHITECTURAL		
STRUCTURAL		
MECHANICAL		
ELECTRICAL		
APPROVED BY		
PROJECT NO.		
SCALE A1:1/50, A3:1/100		
DATE		
DRAWING NO. A-13		
SHEET NO.		
BUILDING NAME		
PROJECT		
DRAWING TITLE 창호 일람표 - 1		

[illegible][illegible]

KEY PLAN

DOOR

WINDOW


NOTES

1. 상호의 치수 및 수량은 평면도상의 치수 및 수량을 우선으로 한다.
2. 상호의(WXH)는 외각치수이므로 제작 설치시 한장 치수를 확인후 설치한다.
3. 내/외부에 직접 노출된 문틀 및 유리 주위에 코킹 처리한다.
4. 모든 부속설치는 해당상호의 무게, 형태, 용도에 적합하여야 하며 전문업체도면에 의거 감동권 승인후 시공한다.
5. 모든 설계류는 1차 방청처리후 마감을 원칙으로한다. (단, 앵커볼트는제외)
6. 콘크리트 부분에 설치하는 프레임 및 부속설치물 등의 설치는 하부에 설치공간 확보후 타일투록 한다.
7. 문의 개폐방법은 평면도를 참조한다.
8. 콘크리트 및 벽돌에 접하는 프레임은 방청처리를 한다.
9. 문 락 : 기성품 사용
10. 커튼박스 SIZE : 'A-24 외벽 부분상세도-2' 참조


■ 창호철물 일람표	
HDW-1(SINGLE DOOR)	HDW-4 (DOUBLE DOOR)
- 2-PIVOT HINGE - LOCK SET - DOOR CLOSER - FLOOR DOME STOP	- 4-FLOOR HINGE (SET) - LOCK SET (DEAD LOCK) - Ø16" SST. 손잡이
HDW-2 (DOUBLE DOOR)	HDW-5(SINGLE DOOR)
- 4-PIVOT HINGE - LOCK SET - DOOR KNOB - DOOR CLOSER - 2-FLUSH BOLT - DUST PROOF STRIKE - 2-FLOOR DOME STOP	- 2-PIVOT HINGE - LOCK SET
	HDW-6(WOOD DOOR)
	- 3-나비정첩 (황동) - LOCK SET - SST. 현틀 손잡이 - WALL DOOR STOPER
HDW-3	
- 2-FLOOR HINGE (SET) - LOCK SET (DEAD LOCK) - Ø16" SST. 손잡이	

■ 창호약어 일람표	
- SD : STEEL DOOR - FSD : FIRERATED STEEL DOOR - SSD : STAINLESS STEEL DOOR - AD : ALUMINIUM DOOR - WD : WOOD DOOR - OHD : OVER HEAD DOOR - HD : HANGER DOOR - RD : ROLL DOOR - SS : STEEL SHUTTER - SPS : STEEL PIPE SHUTTER - FSS : FIRERATED STEEL SHUTTER - SSS : STAINLESS STEEL SHUTTER - SSPS : STAINLESS STEEL PIPE SHUTTER - AS : ALUMINIUM SHUTTER - SL : SLAB LEVEL	- SW : STEEL WINDOW - SSW : STAINLESS STEEL WINDOW - AW : ALUMINIUM WINDOW - WW : WOOD WINDOW - SG : STEEL GRILL - SSG : STAINLESS STEEL GRILL - AG : ALUMINIUM GRILL - WG : WOOD GRILL - MFR : MANUFACTURER - HDW : HARDWARE - SSR : STAINLESS STEEL RIB - WR : WOOD RIB - TFW : PLASTIC WINDOW - PF : PLASTIC FRAME


NOTES		
이 도면은 고려전산(주)의 프로그래밍 교육용으로 작성된 도면입니다. 이 도면의 저작권은 고려전산(주)에 있으며 사전 승인 없이 무단 전재 및 재배포할 경우, 관련 법령에 의거 제재를 받을 수 있습니다. 또한, 본사의 교육 이외 용도로의 사용을 금합니다.		
REV. NO.	DATE	REVISION DESCRIPTION
DRAWN BY		
DESIGNED BY		
CHECKED BY		
CIVIL ENGINEERING		
ARCHITECTURAL		
STRUCTURAL		
MECHANICAL		
ELECTRICAL		
APPROVED BY		
PROJECT NO.		
SCALE NONE		
DATE		
DRAWING NO. A-14		
SHEET NO.		
BUILDING NAME		
PROJECT		
DRAWING TITLE 창호 일람표 - 2		

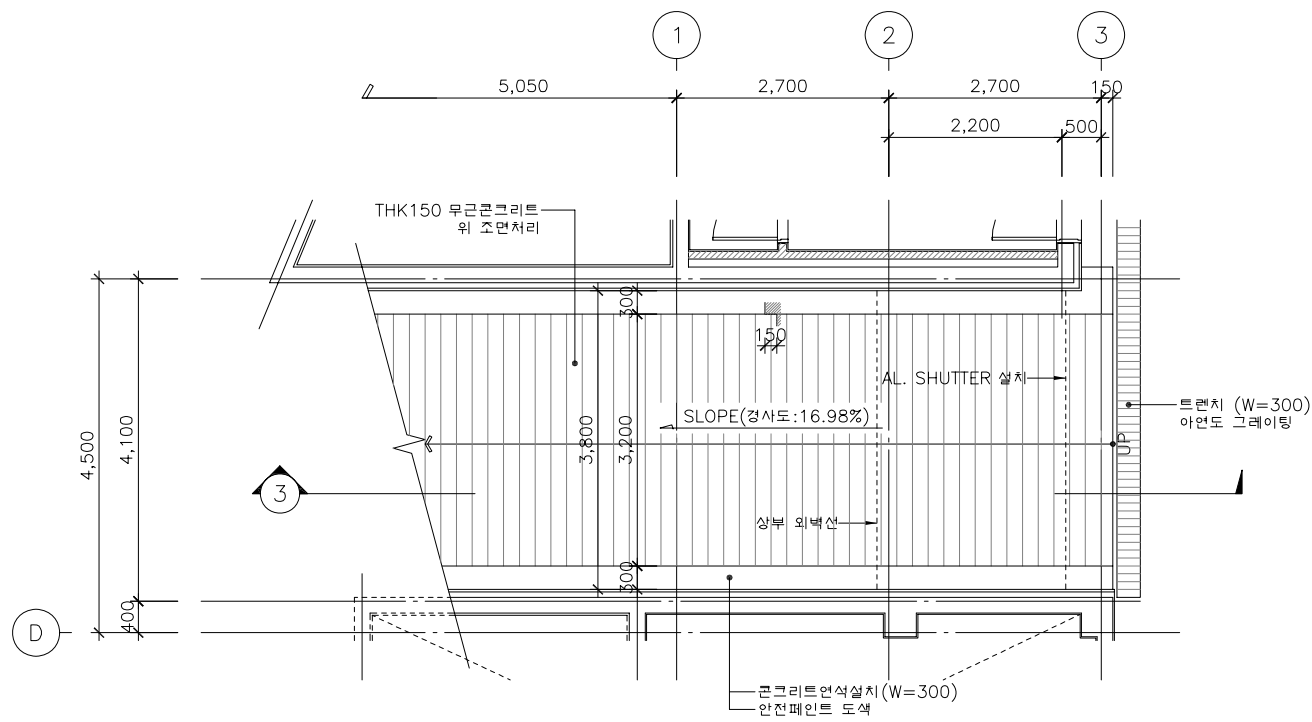

1 지상층 경사로 평면도
축척 : 1/100

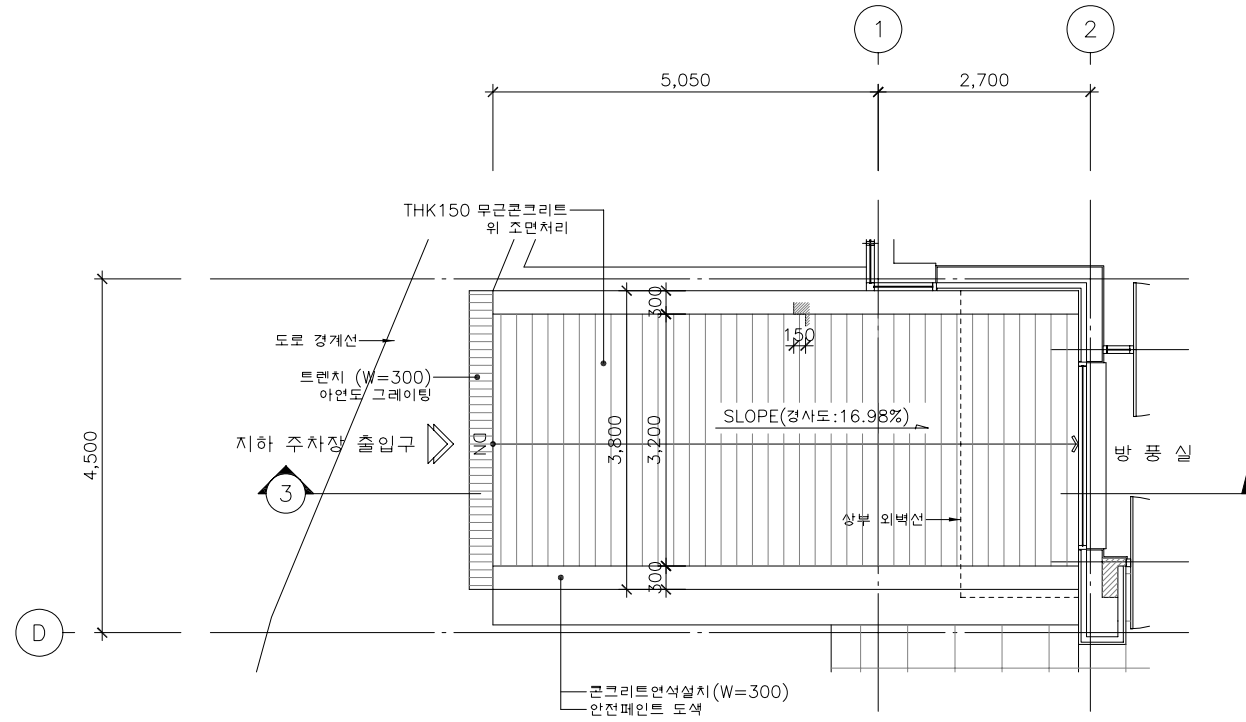

2 지상층 경사로 평면도
축척 : 1/100

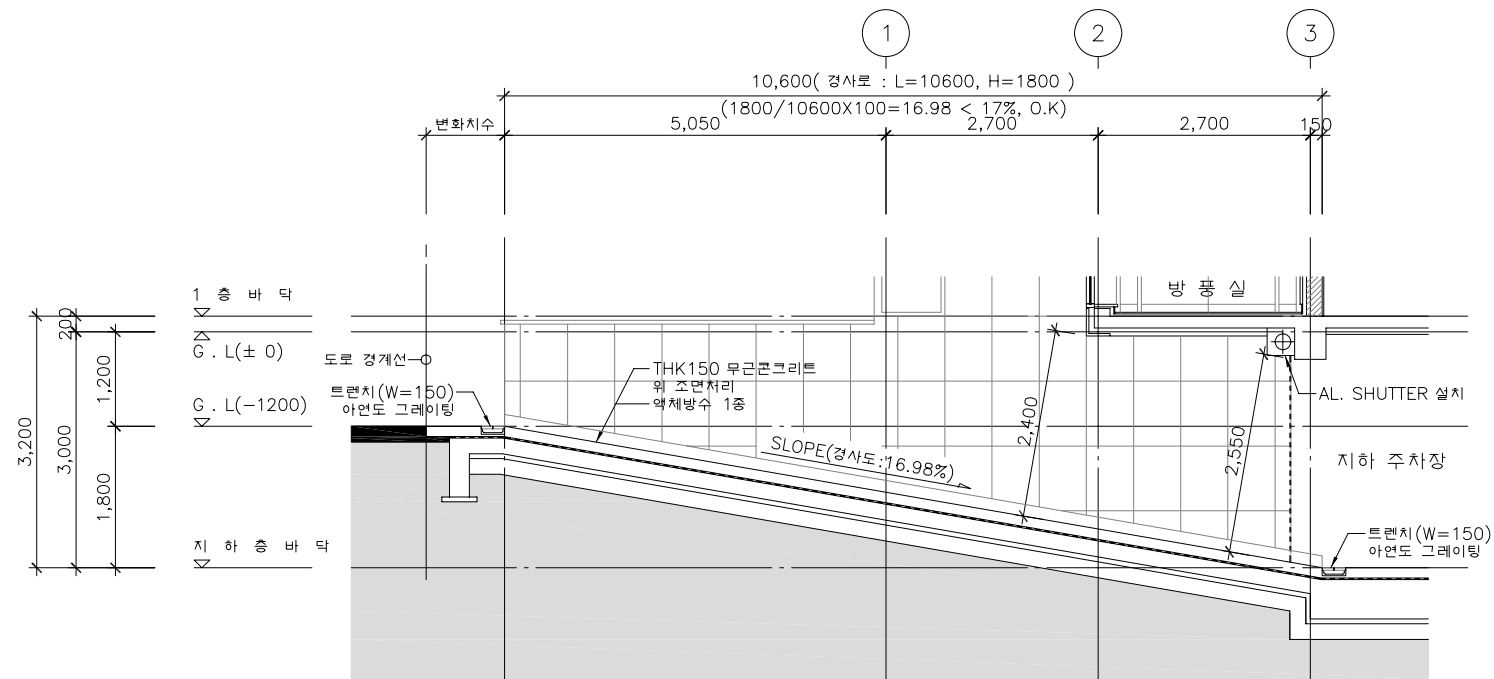


3 경사로 단면도
축척 : 1/100

NOTES

이 도면은 고려전산(주)의 프로그램 교육용으로 작성된 도면입니다.

이 도면의 저작권은 고려전산(주)에 있으며 사전 승인 없이 무단전제 및 재배포할 경우, 관련 법령에 의거 제재를 받을 수 있습니다. 또한, 본사의 교육 이외 용도로의 사용을 금합니다.

REV. NO.	DATE	REVISION DESCRIPTION
DRAWN BY		
DESIGNED BY		
CHECKED BY		
CIVIL ENGINEERING		
ARCHITECTURAL		
STRUCTURAL		
MECHANICAL		
ELECTRICAL		
APPROVED BY		
PROJECT NO.		
SCALE A1:1/50, A3:1/100		
DATE		
DRAWING NO. A-15		
SHEET NO.		
BUILDING NAME		
PROJECT		
DRAWING TITLE 경사로 평/단면도		

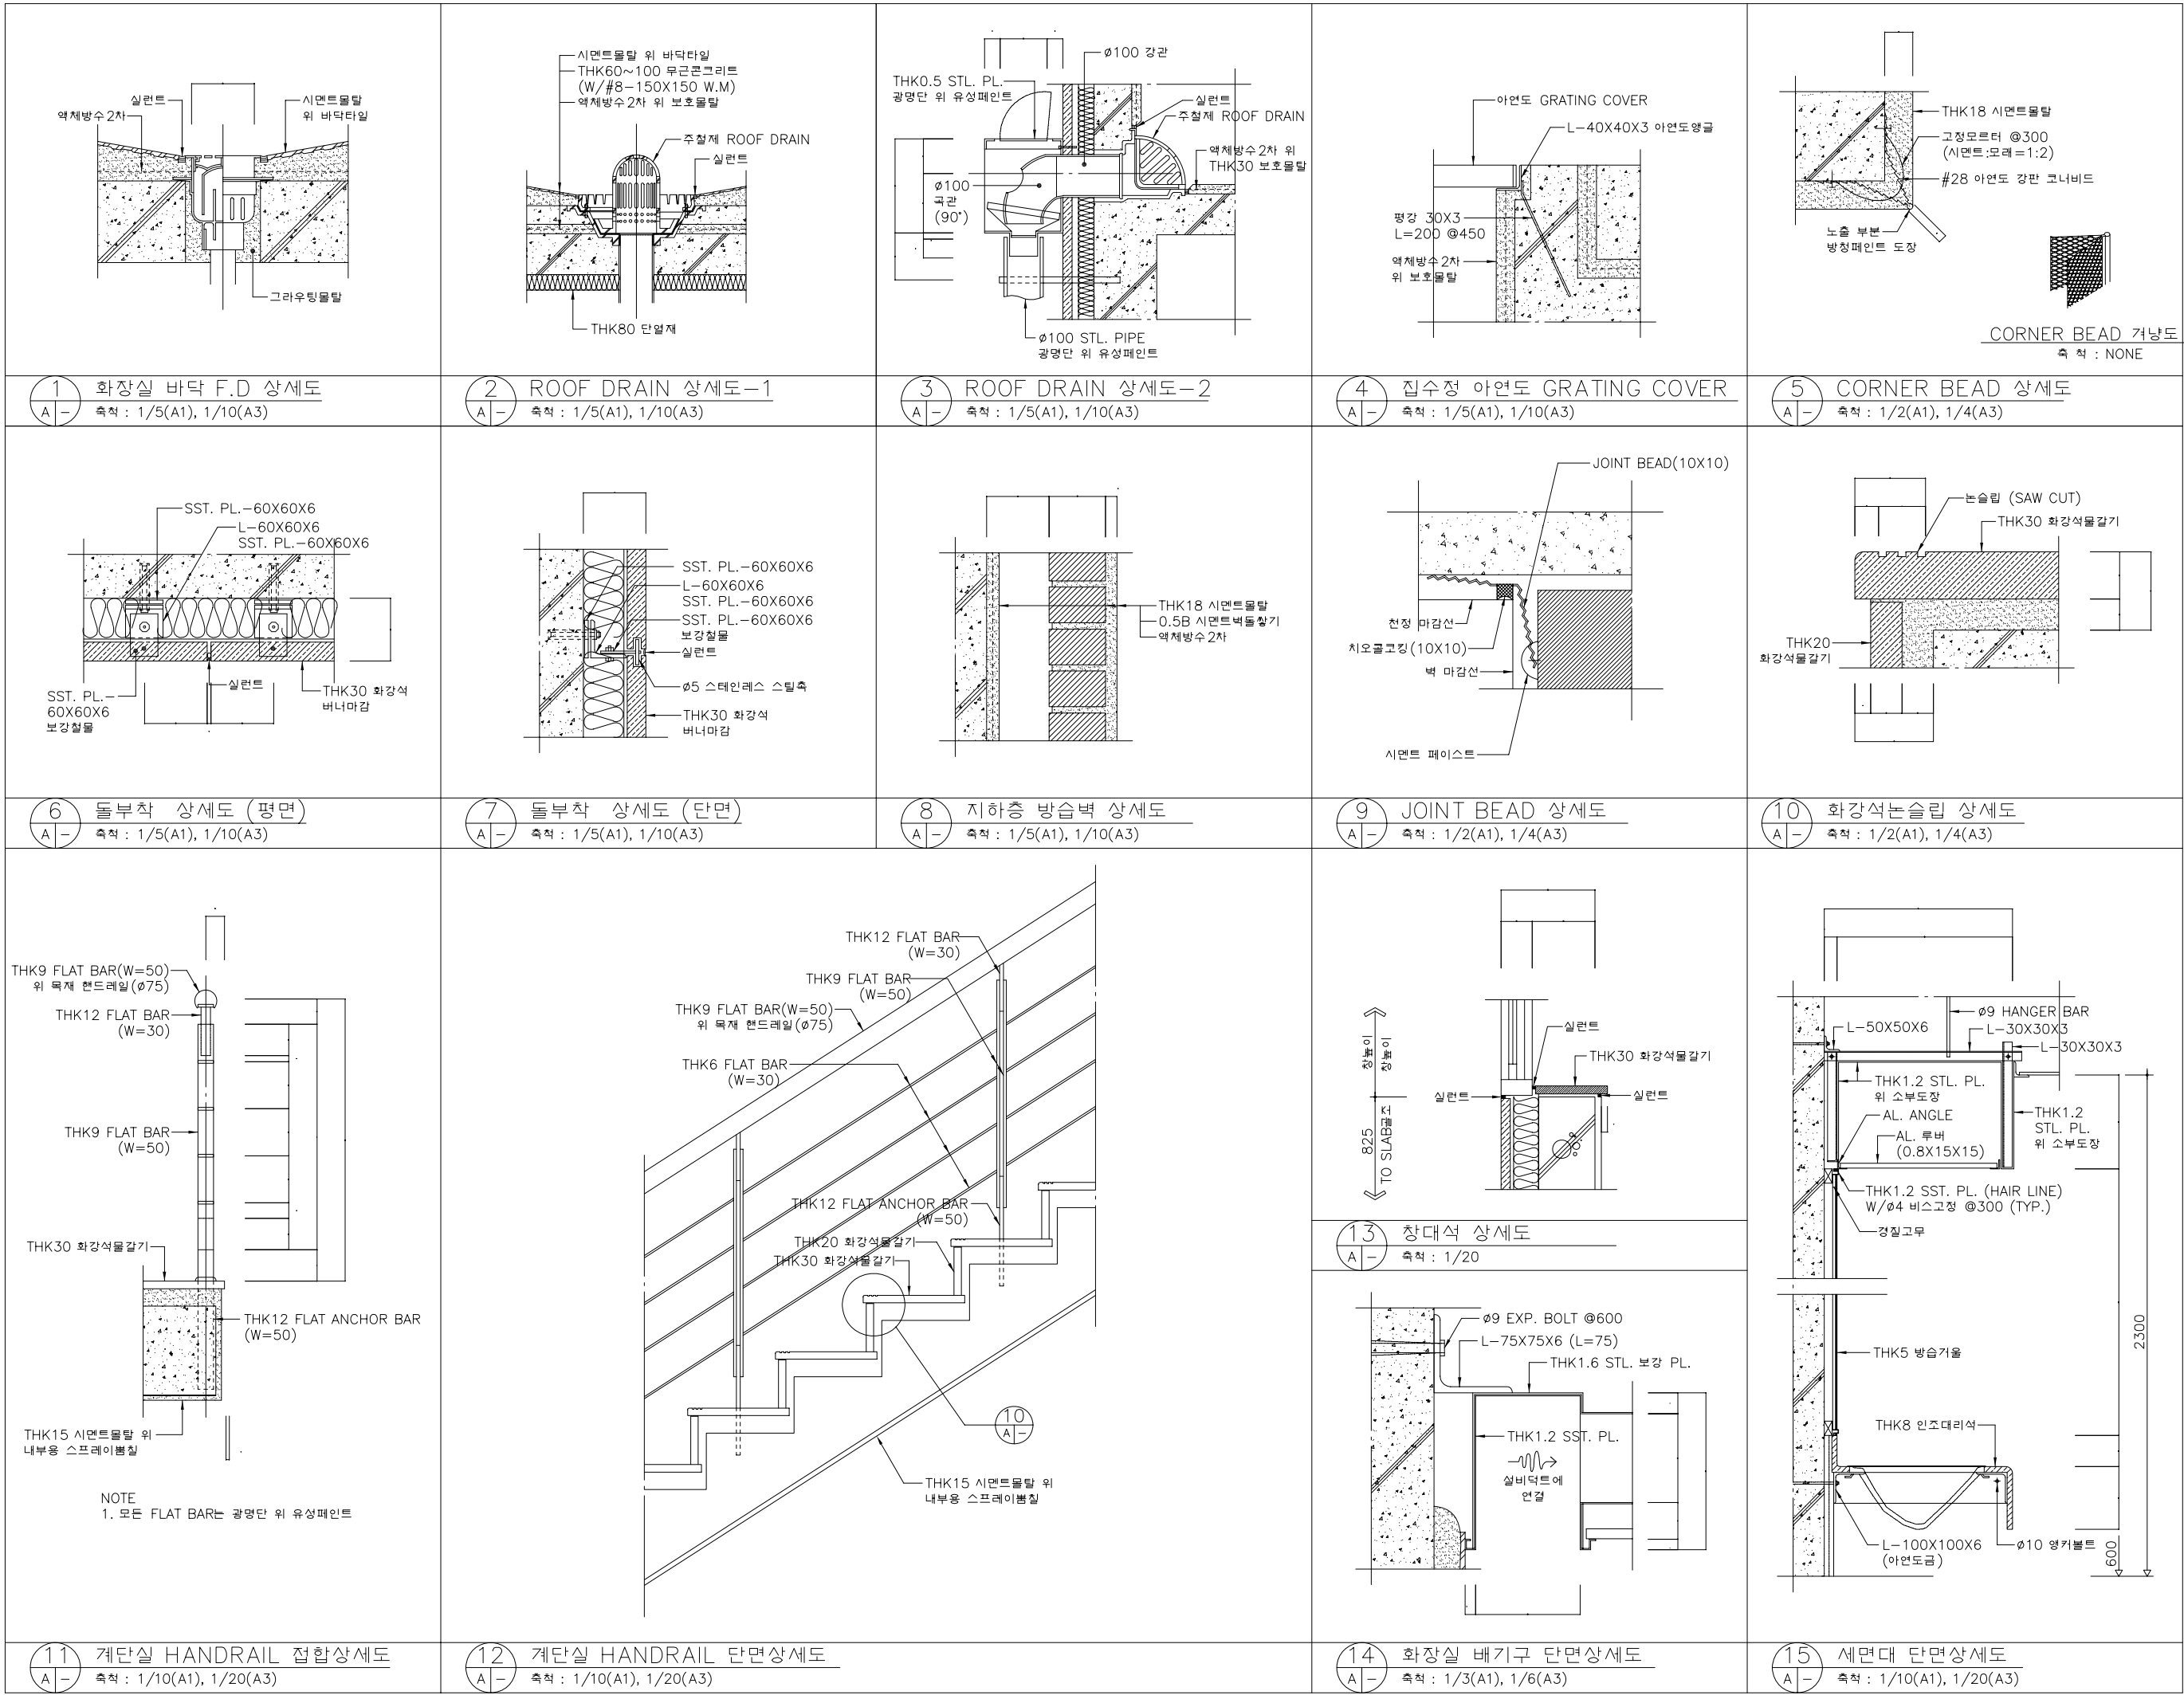

NOTES

이 도면은 고려전산(주)의 프로그램 교육용으로 작성된 도면입니다.

이 도면의 저작권은 고려전산(주)에 있으며 사전 승인 없이 무단전제 및 재배포할 경우, 관련 법령에 의거 제재를 받을 수 있습니다. 또한, 본사의 교육 이외 용도로의 사용을 금합니다.

REV. NO.	DATE	REVISION DESCRIPTION
----------	------	----------------------

DRAWN BY

DESIGNED BY

CHECKED BY

CIVIL ENGINEERING

ARCHITECTURAL

STRUCTURAL

MERCHANICAL

ELECTRICAL

APPROVED BY

PROJECT NO.

SCALE

DATE

DRAWING NO.



SHEET NO.

BUILDING NAME

PROJECT

DRAWING TITLE


부분 상세도 - 1

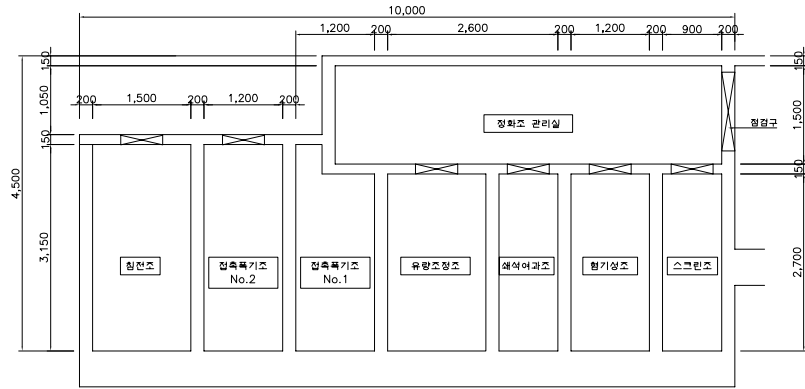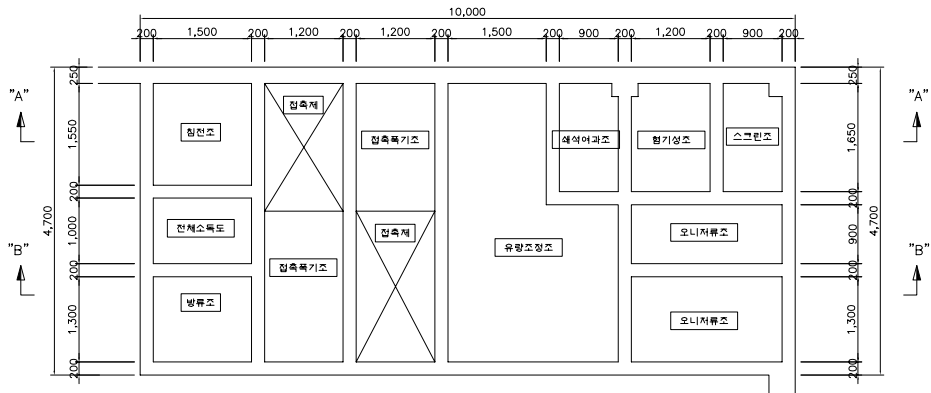

SECTION "A"—"A"

작 도		TITLE NAME						평 면 도
N/S								
작성일	작성	조 시	설 계	관 리	승 인	PROJECT TITLE		

작 도		TITLE NAME						SECTION "A"—"A"
N/S								
작성일	작성	조 시	설 계	관 리	승 인	PROJECT TITLE		

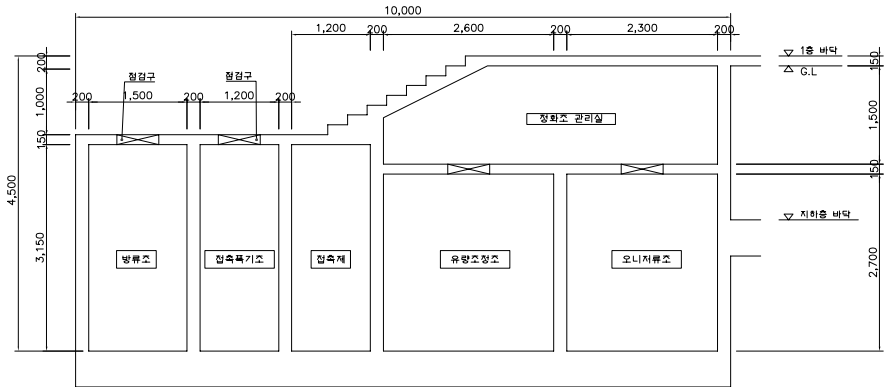

SECTION "B"—"B"

작 도		TITLE NAME						FLOW-SHEET
N/S								
작성일	작성	조 시	설 계	관 리	승 인	PROJECT TITLE		

작 도		TITLE NAME						SECTION "B"—"B"
N/S								
작성일	작성	조 시	설 계	관 리	승 인	PROJECT TITLE		

NOTES

이 도면은 고려전산(주)의 프로그램 교육용으로 작성된 도면입니다.

이 도면의 저작권은 고려전산(주)에 있으며 사전 승인 없이 무단전재 및 재배포할 경우, 관련 법령에 의거 제재를 받을 수 있습니다. 또한, 본사의 교육 이외 용도로의 사용을 금합니다.

REV. NO.	DATE	REVISION DESCRIPTION
----------	------	----------------------

DRAWN BY

DESIGNED BY

CHECKED BY

CIVIL ENGINEERING

ARCHITECTURAL

STRUCTURAL

MERCHANICAL

ELECTRICAL

APPROVED BY

PROJECT NO.

SCALE
NONE

DATE

DRAWING NO.
A-18

SHEET NO.

BUILDING NAME

PROJECT

DRAWING TITLE

정 화 조